



Bouwlocatie:
Hertog van Beijerenstraat - Ter Aar
Kadastrale gemeente: Ter Aar
Sectie: A
Perceelnummer: 8356 - 9506
Totaal bebouw oppervlak = 3679m²

Parkeren:
Zie door opdrachtgever opgestelde "motivatieve afwijking parkeernorm"

Elektrische laadpaal:
Minimaal 20% van de parkeerplaatsen is voorzien van een mantelbuis t.b.v. toekomstige laadpalen

Opstelplaatsen hulpverleningsdiensten:
Voldoen aan bouwbesluit 2012 art. 6.37:

- a. een breedte van ten minste 4,5 meter
- b. een verharding over een breedte van ten minste 3,25 meter, die geschikt is voor motorvoertuigen met een massa van ten minste 14.500 kilogram
- c. een vrijgehouden hoogte boven de kruin van de weg van ten minste 4,2 meter en
- d. een doeltreffende afkapping.

Deze tekening niet gebruiken voor uitvoering van enige werkzaamheden.
Staalconstructie- en funderingsberekeningen volgens opgaaf constructeur.
Bouwbesluittoetsing en BENG berekening volgens nader in te dienen rapportage

NEN-NORMERING:	
Constructieve veiligheid:	NEN-EN 1995-1-1
Brandbeperking vluchtroutes:	NEN 13501-1
Inbrandveerendheid:	NEN 5987/5096
Gevelbescherming:	NEN 5077
Vochtweringsgrenswaarde:	NEN 2778
Afvoer vuilwater/hemelwater:	NEN 3215/7013
Luchtverversing:	NEN 1087/8087
Verbrandingsvluchtoverloop/ontlastingshoor:	NEN 2767/6002
Materialen:	NEN 2768
Thermische isolatie:	NTA 8800
Luchtdoorlatendheid:	NEN 2686
Energieprestatie:	NTA 8800
Drinkwater-installatie:	NEN 1006
Electra-installatie:	NEN 1010/1041
CV-installatie:	NEN 3026/1078

INSTALLATIES:
Alle installaties, zoals (rood)verlichting, water, riolering, enz. uitvoeren conform opgaaf en tekeningen van installateur.

INTERGRIEPE TOEGANGELIJKHEID:
De vrije doorgang van alle toegangen tot ruimtes dient minimaal 850x2100mm te zijn, conform BBL art. 4.102 lid 1.
Daarbij is de opstaphoogte bij entree deuren niet groter dan 20mm, conform BBL art. 4.102 lid 5

WERING MUZEN EN RATTEN:
Openingen in fundering, voor, dak en wand zijn "muisdicht" (conform BBL art. 4.144 en 4.145)

GEBOUWGEVEGENS:	
Bebouwd oppervlak:	GBO / VG GBO+GR: 3679m²
Bruto inhoud:	34689m³
Bruto vloeroppervlak (GB):	38.5m²
GB Lichte ind. functie:	2327.4m²
VG Lichte ind. functie:	2349.5m²
GB Industriële functie:	1595.4m²
VG Industriële functie:	1610.6m²
GB Kantoorfunctie:	74.2m²
VG Kantoorfunctie:	74.7m²
GB Bijkantoorfunctie:	40.3m²
VG Bijkantoorfunctie:	40.3m²

Opdrachtgever:
Logistiek Behaer B.V.
Wildebeestweg 124
7345 CG Wierum Wiesel

Bouwadres:
Hertog van Beijerenstraat 2
2401 EM Ter Aar

Onderwerp:
Situatie

VEILIGHEIDSMATREGELEN:	
PS	Deur welke, over de minimaal vereiste breedte, zonder gebruik te maken van een sleutel, kan worden geopend. Dit is u.a. draaioverloop of opsluitering.
1	Vluchtweg aanduidingsbord / transparant verlichtingsmatras, uitvoering van de symbolen "UIT" en "NOODUITGANG" conform de pictogrammen zoals vermeld in de NEN 3011 / NEN-EN ISO 7243 en de zichtbaarheidsafstand conform de NEN-EN 1835.
2	Spiegelkast met een inhoud van ten minste 6 liter schuim.
3	Brandingsramp met een slangenlengte van 30m.
4	Deur welke zelfsluitend is uitgevoerd, en in combinatie met het kozijn een brandwerendheid bezit van ten minste 60 minuten (conform NEN 1089).
5	60 minuten weerstand tegen brandweering en brandisolatie (WBO) conform de NEN 6008 of NEN-EN 13501-2.
6	Brandwerende wandpanelen (EWB) en 60 minuten brandwerende staalconstructie.

Tussen de assen 34, EF en LK wordt een gebouwwand geplaatst met aan beide zijden een op zichzelf staande draaioverloop.

De gebouwwand is opgebouwd uit een constructie met een weerstand van ten minste 60 minuten brandweering en brandisolatie (WBO) conform de NEN 6008 of NEN-EN 13501-2.

Postbus 378
3900 AJ VEENENDAAL
T: 0318 - 521700
F: 0318 - 520418
E: info@hardeman.nl







Tekenaar: NVV
Datum: 07 maart 2025
Schaal: 1:500
Formaat: A0

Wijziging:
Wijziging:
Wijziging:
Wijziging:
Wijziging:

Onderwerp:
Situatie

Werknummer:
44449

Bidnummer:
1

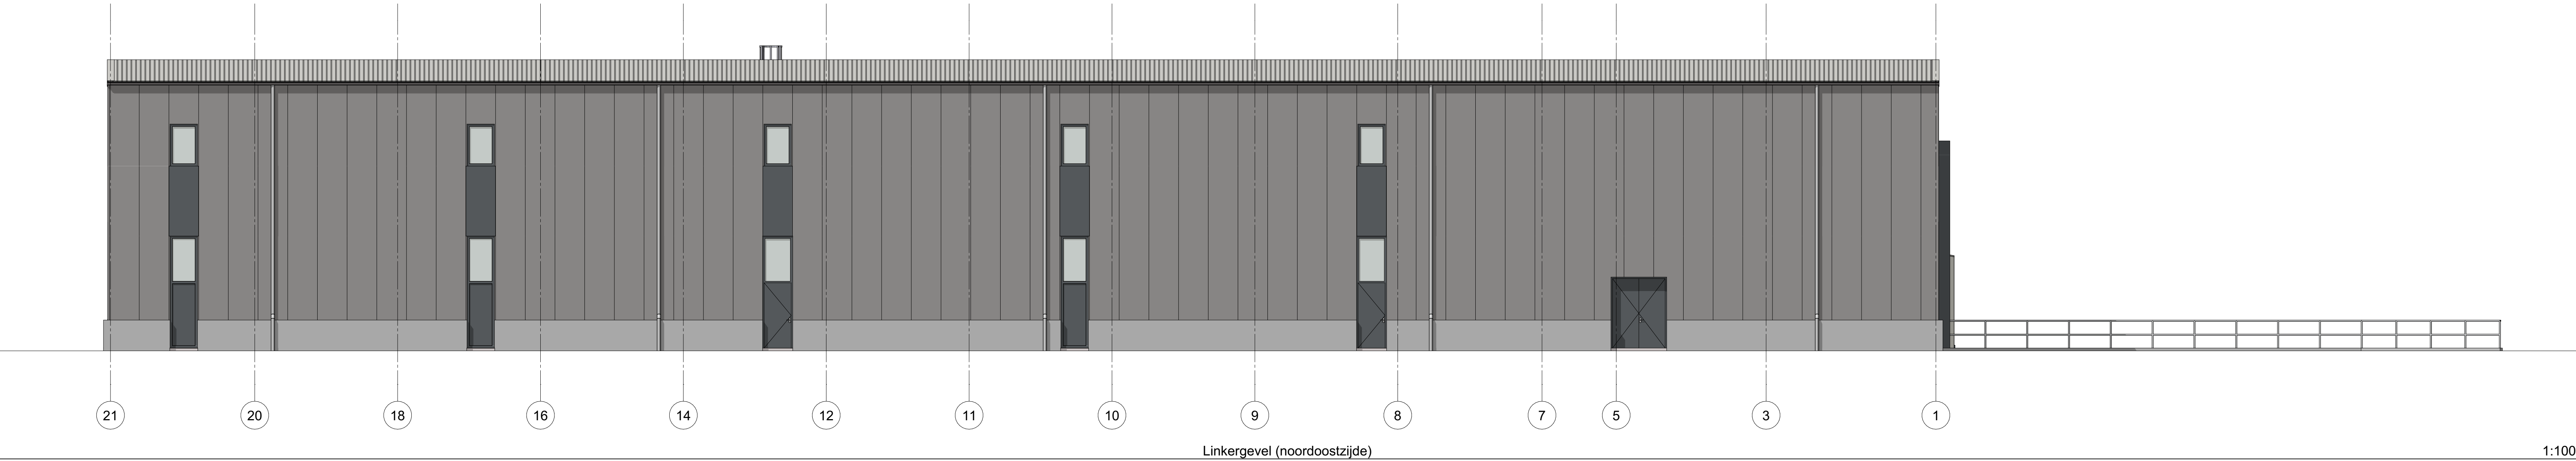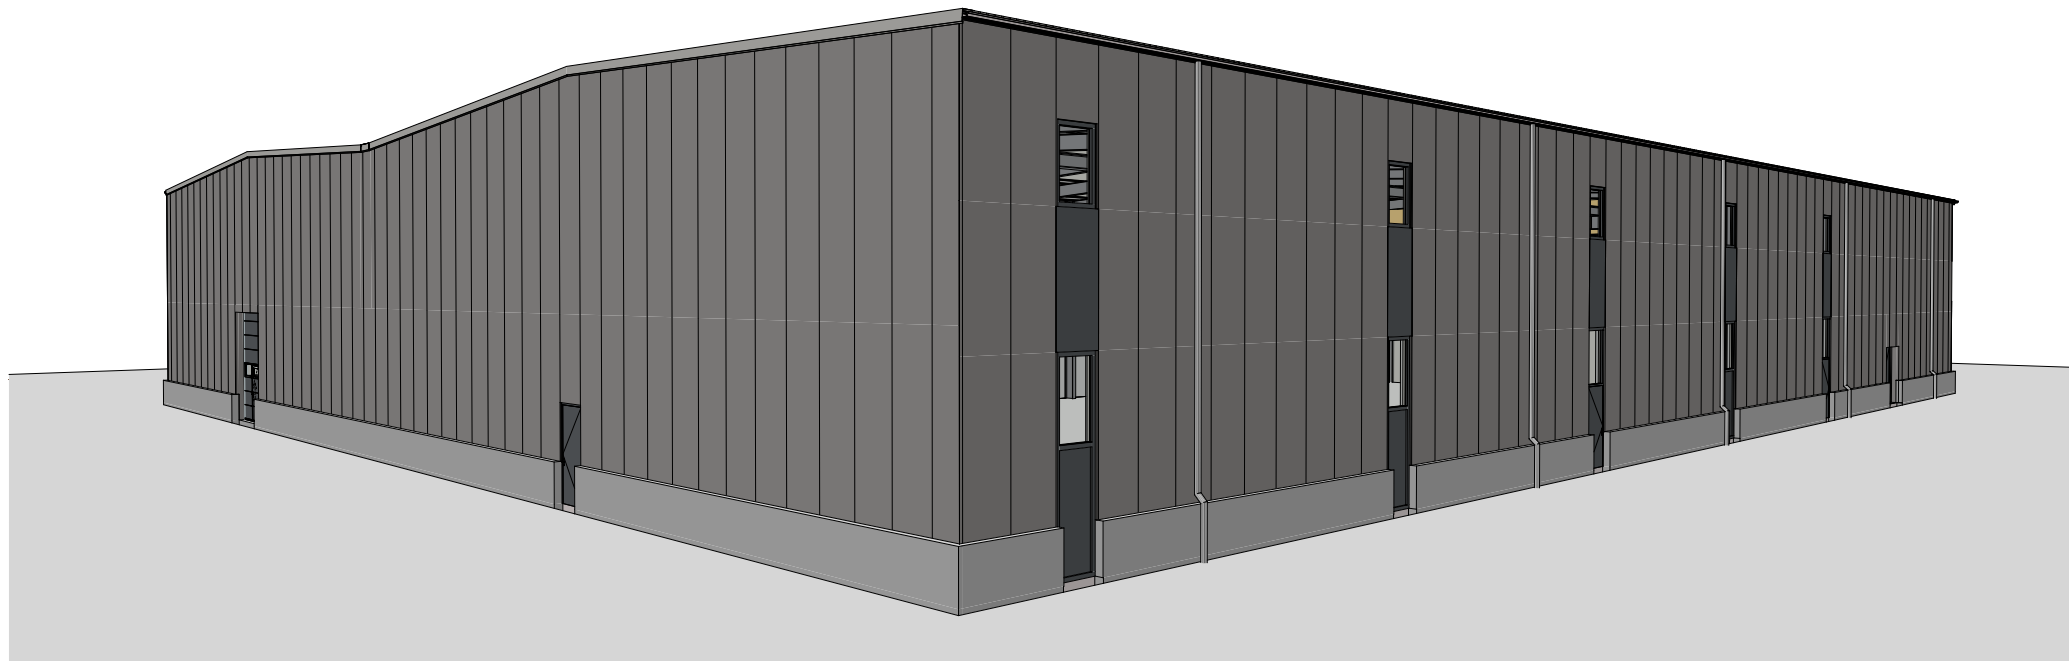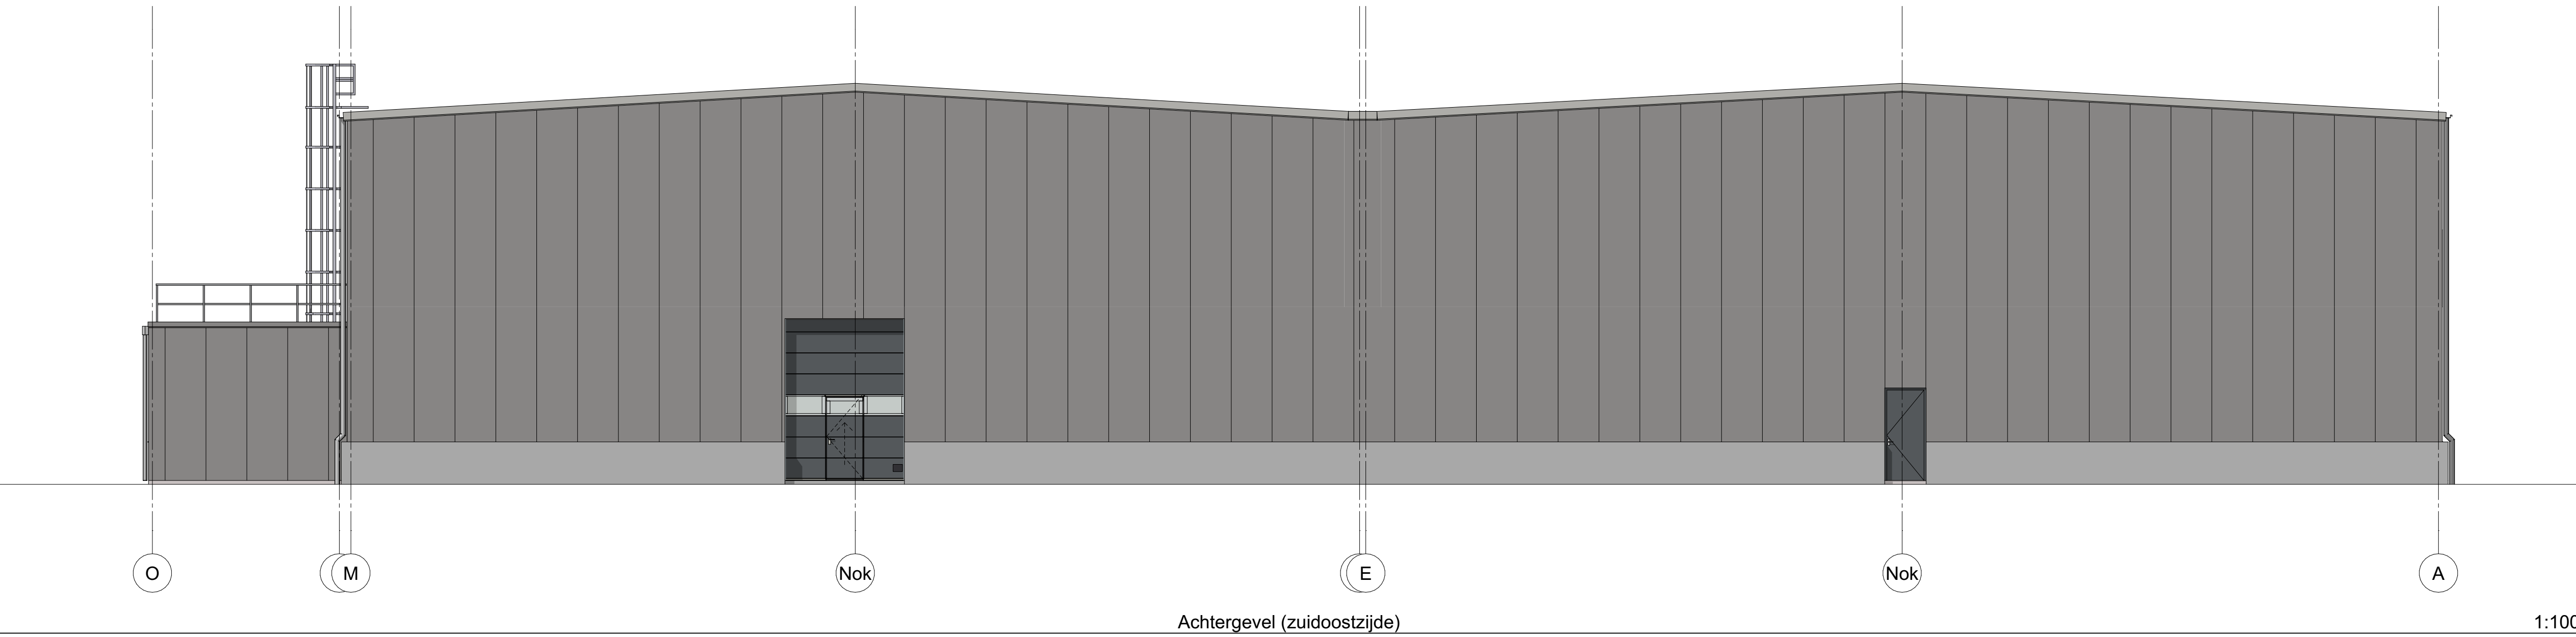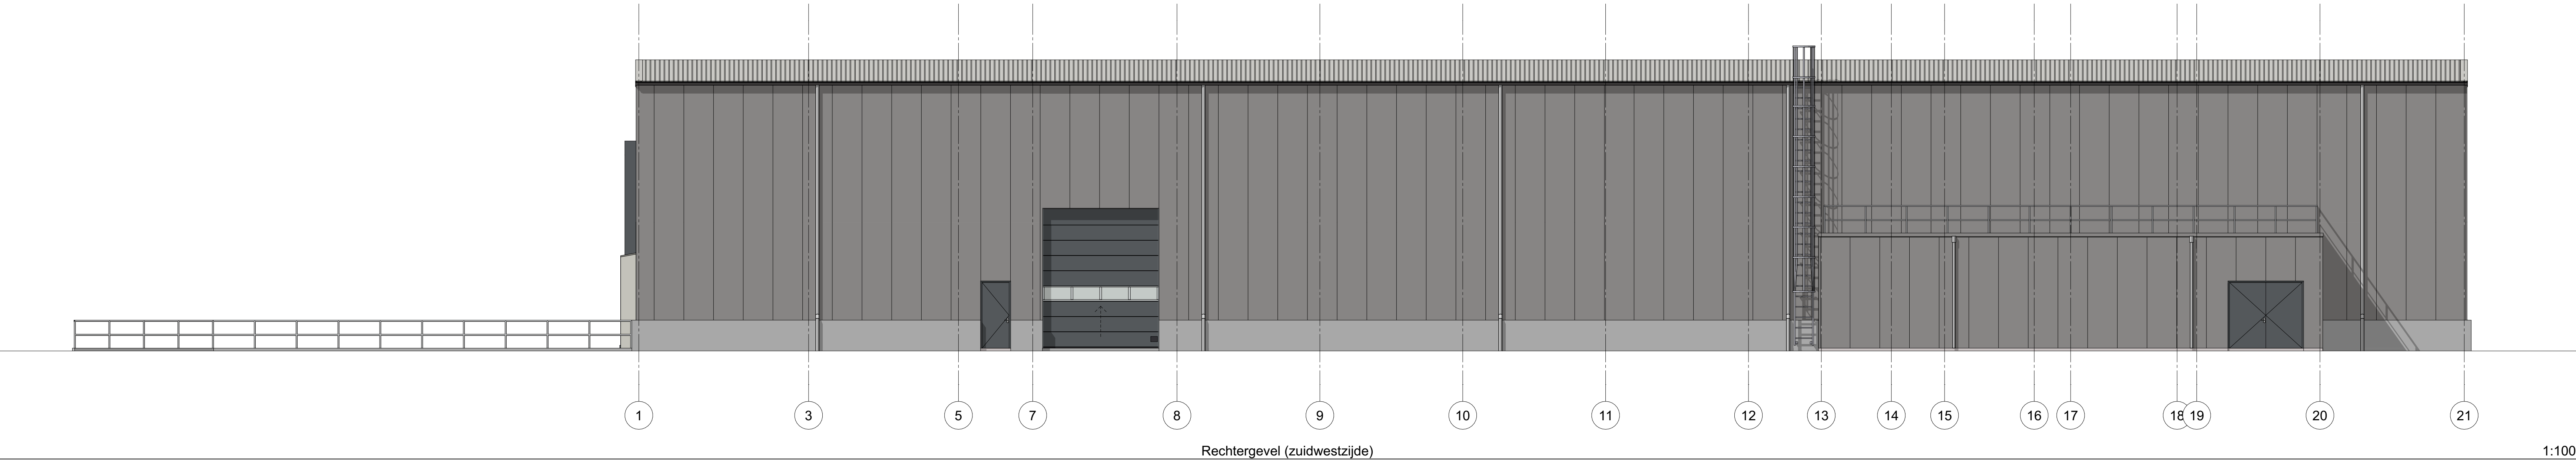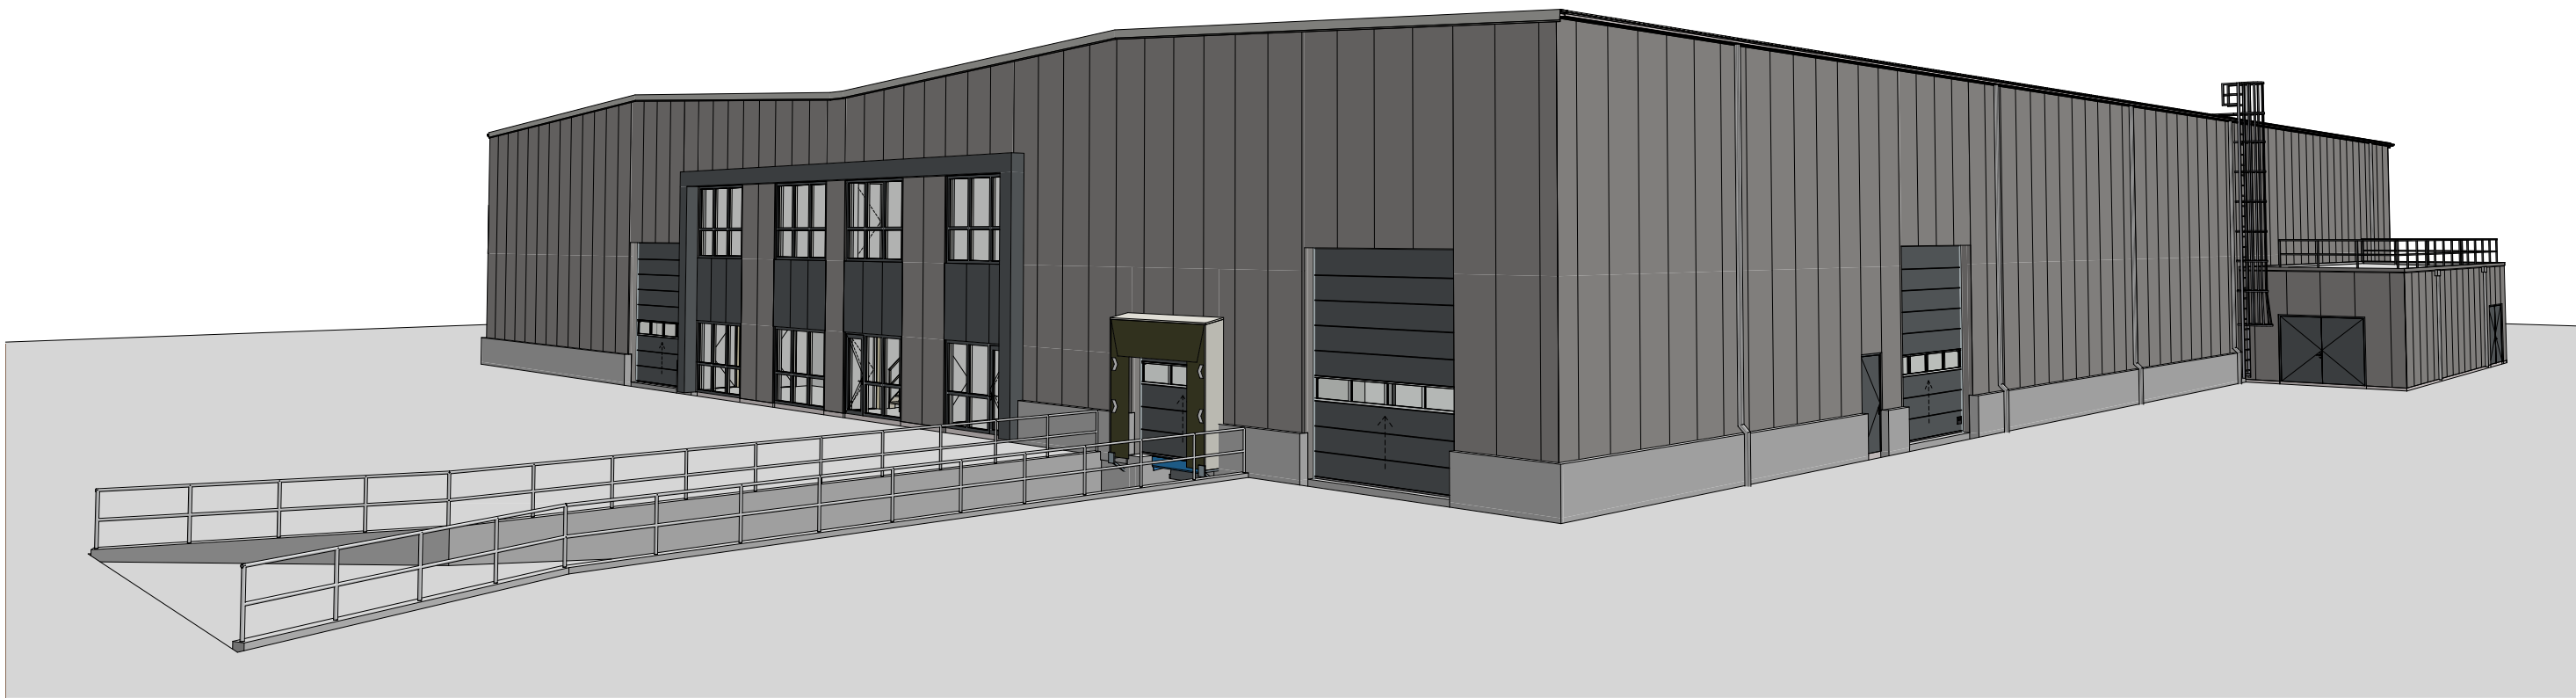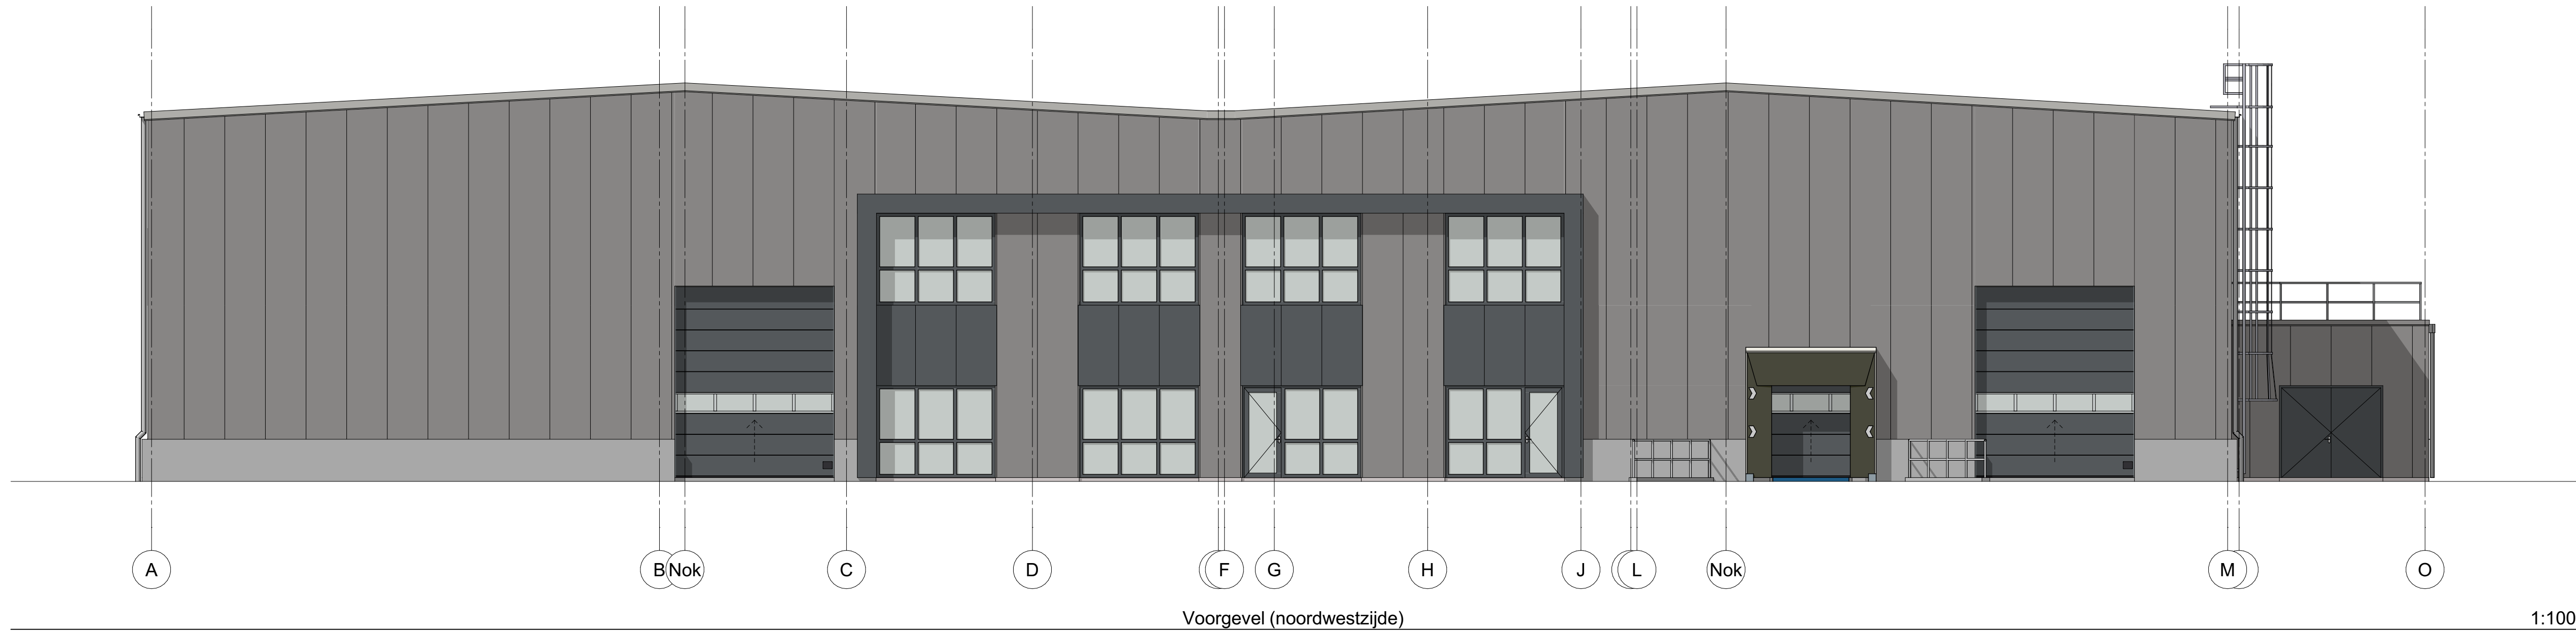

Deze tekening niet gebruiken voor uitvoering van enige werkzaamheden.
Staalconstructie- en funderingsberekeningen volgens opgaaf constructeur.
Bouwbesluittoetsing en BENG berekening volgens nader in te dienen rapportage

NEN-NORMERING:
Constructieve veiligheid: NEN-EN 1993-1-1:1999
Brandbeperking vluchtroutes: NEN 13501-1
Inbrandveerendheid: NEN 5987/5096
Geluidsbescherming: NEN 5077
Vochtweringsgeveerendheid: NEN 2778
Afvoer vuilwater/hemelwater: NEN 3215/7013
Luchtverversing: NEN 1087/8087
Verbrandingsglutlichtboven/ rookgasafvoer: NEN 2767/6002
Materialen: NEN 2768
Thermische isolatie: NTA 8800
Luchtdoorlatendheid: NEN 2686
Energieprestatie: NTA 8800
Drinkwater-installatie: NEN 1006
Electra-installatie: NEN 1010/1041
CV-installatie: NEN 3026/1078

INSTALLATIES:
Alle installaties, zoals (rood)verlichting, water, riolering, enz. uitvoeren conform opgaaf en tekeningen van installateur.

INTEGRALE TOEGANKELIJKHEID:
De vrije doorgang van alle toegangen tot ruimtes dient minimaal 850x2100mm te zijn, conform BBL art. 4.102 lid 1.
Daarbij is de opstaphoogte bij entree-deuren niet groter dan 20mm, conform BBL art. 4.102 lid 5.

WERING MUZEN EN RATTEN:
Oopeningen in fundering: voor, dak en wand zijn "muisdicht" (conform BBL art. 4.144 en 4.145).

GEBOUWGEVEGENS:
Bebouwd oppervlak: GBO / VG GRO+GR: 3073m²
Bruto inhoud: 34689m³
Gem. ruiswaarde (GR): 38.5m²
GBO Lichte Ind. functie: 2327.4m² 2349.5m²
VG Lichte Ind. functie: 8m²
GBO Industriële functie: 1595.4m² 1610.6m²
VG Industriële functie: 1595.4m²
GBO Kantoorfunctie: 74.0m² 74.7m²
VG Kantoorfunctie: 74.0m²
GBO Bijkantoorfunctie: 49.3m² 49.3m²
VG Bijkantoorfunctie: 49.3m²

VEILIGHEIDSMATREGELEN:
PS Deur welke, over de minimaal vereiste breedte, zonder gebruik te maken van een sleutel, kan worden geopend. Of d.m.v. draaiknop/inloof of gelijkwaardig.
1 Vuchtweg aanduidingsbord / transparant verlichtingsarmatuur, uitvoering van de symbolen "UIT" en "NOODUITGANG" conform de pictogrammen zoals vermeld in de NEN 3611 / NEN-EN ISO 7010 en de zichtbaarheidsklassen conform de NEN-EN 1835.
2 Brandstrijdkap met een inhoud van ten minste 6 liter schuim.
3 Brandstrijkapparaat met een slanglengte van 30m.
4 Deur welke zelfsluitend is uitgevoerd, en in combinatie met het kozijn een brandwerendheid bezit van ten minste 60 minuten (conform NEN 6069).
5 60 minuten weersstand tegen brandwerendheid en branddoornslag (WED60), conform de NEN 6068 of NEN-EN 13501-2.
6 Brandwerende wandpanelen (EW60) en 60 minuten brandwerende staalconstructie.
Tussen de assen 34, E-F en L-K wordt een gasbetonwand geplaatst met aan beide zijden een 60 minuten weersstand tegen brandwerendheid, zodat bij brand in één van de zijdecompartimenten de gasbetonwand minimaal 60 minuten dicht staat waardoor de WED60 van 60 minuten tussen de compartimenten gewaarborgd is.
CV-as 20 (tussen M en O) en op as M (tussen 18 en 21) worden 100mm Plaatstalen brandwerende wandpanelen (EW60). De dakflaten worden op de assen worden 60 minuten brandwerend uitgevoerd en voorzien van een zogenaamd "brandwerende constructie" (WED60 + 60 minuten o.v.v. spiegelarmatuur).

Materialen bopposit aan de binnenzijde van een schacht, kader of kanaal voldoet minimaal aan de in BBL art. 4.33 gestelde voorwaarde (bepaald conform NEN-EN 13501-1).
Een zijde van een constructieonderdeel die grenst aan de binnenruimte voldoet minimaal aan de in BBL art. 4.43 gestelde brand- en rookklasse (bepaald conform NEN-EN 13501-1).
Een zijde van een constructieonderdeel die grenst aan de buitenruimte voldoet minimaal aan de in BBL art. 4.44 gestelde brand- en rookklasse (bepaald conform NEN-EN 13501-1).
Uitvoering van de brand- en rookklasse van het dak (uitvoering conform BBL art. 4.47).
Een beklopbaar dak (binnenzijde van een vloer, een trap, een hellingplaat), voldoet min. aan de in BBL art. 4.45 gestelde brand- en rookklasse (conform NEN-EN 13501-1).
Elektrische ledijnen en pijpleidingen voldoen minimaal aan de in BBL art. 4.46 gestelde brand- en rookklasse (bepaald conform NEN-EN 13501-1 en NEN-EN 13501-6).
De weersstand tegen rookdoorgang voldoet minimaal aan de in BBL art. 4.61 en art. 4.62 gestelde eisen (bepaald conform NEN 6075).
De aanwezigheid en uitvoering van een brandmeldinstallatie voldoet minimaal aan de in BBL art. 4.36 gestelde voorwaarde (bepaald conform NEN 2535).
De aanwezigheid en uitvoering van een ontruimingsinstallatie voldoet minimaal aan de in BBL art. 4.75 gestelde voorwaarde (bepaald conform NEN 2575).

MATERIALEN EN KLEUREN:
Onderdeel: Materiaal: Kleur: Kleurcode:
Dak: Staal / PVC Lichtgrijs RAL 7038 / N.v.t.
Dakrand / Windwens: Staal RAL 7037 / RAL 7038
Wanden: Staal Grijsmetaallic RAL 9007
Aanbouwconstructies: Staal RAL 7016
Sierlijsten: Aluminium Antraciet RAL 7016
Borstelwerk: Staal Antraciet RAL 7016
Korpijnen: Kunststof Antraciet RAL 7016
Deuren / Ramen: Kunststof Antraciet RAL 7016
Overheersdeuren: Staal Antraciet RAL 7016
Galen (t.w.a. v.): Aluminium / PVC Grijs / Grijs RAL 7038 / N.v.t.

Opdrachtgever:
Logivest Beheer B.V.
Willemsweg 124
7345 CG Wierum Wiesel


Bouwadres:
Herfing van Beijerenstraat 2
2401 EM Ter Aar

Onderwerp:
Gevelaanzichten

Tekenaar: NVV
Datum: 07 maart 2025
Schaal: 1:100
Formaat: A3
Wijziging:
Wijziging:
Wijziging:
Wijziging:
Wijziging:

HARDEMAN
VEENENDAAL
Postbus 376
3900 AJ VEENENDAAL
Gemeentestraat 2
3903 LH VEENENDAAL
T: 0316 - 521700
F: 0316 - 520418
E: info@hardeman.nl
www.hardeman.nl

Werknummer:
44449
Bodnummer:
2

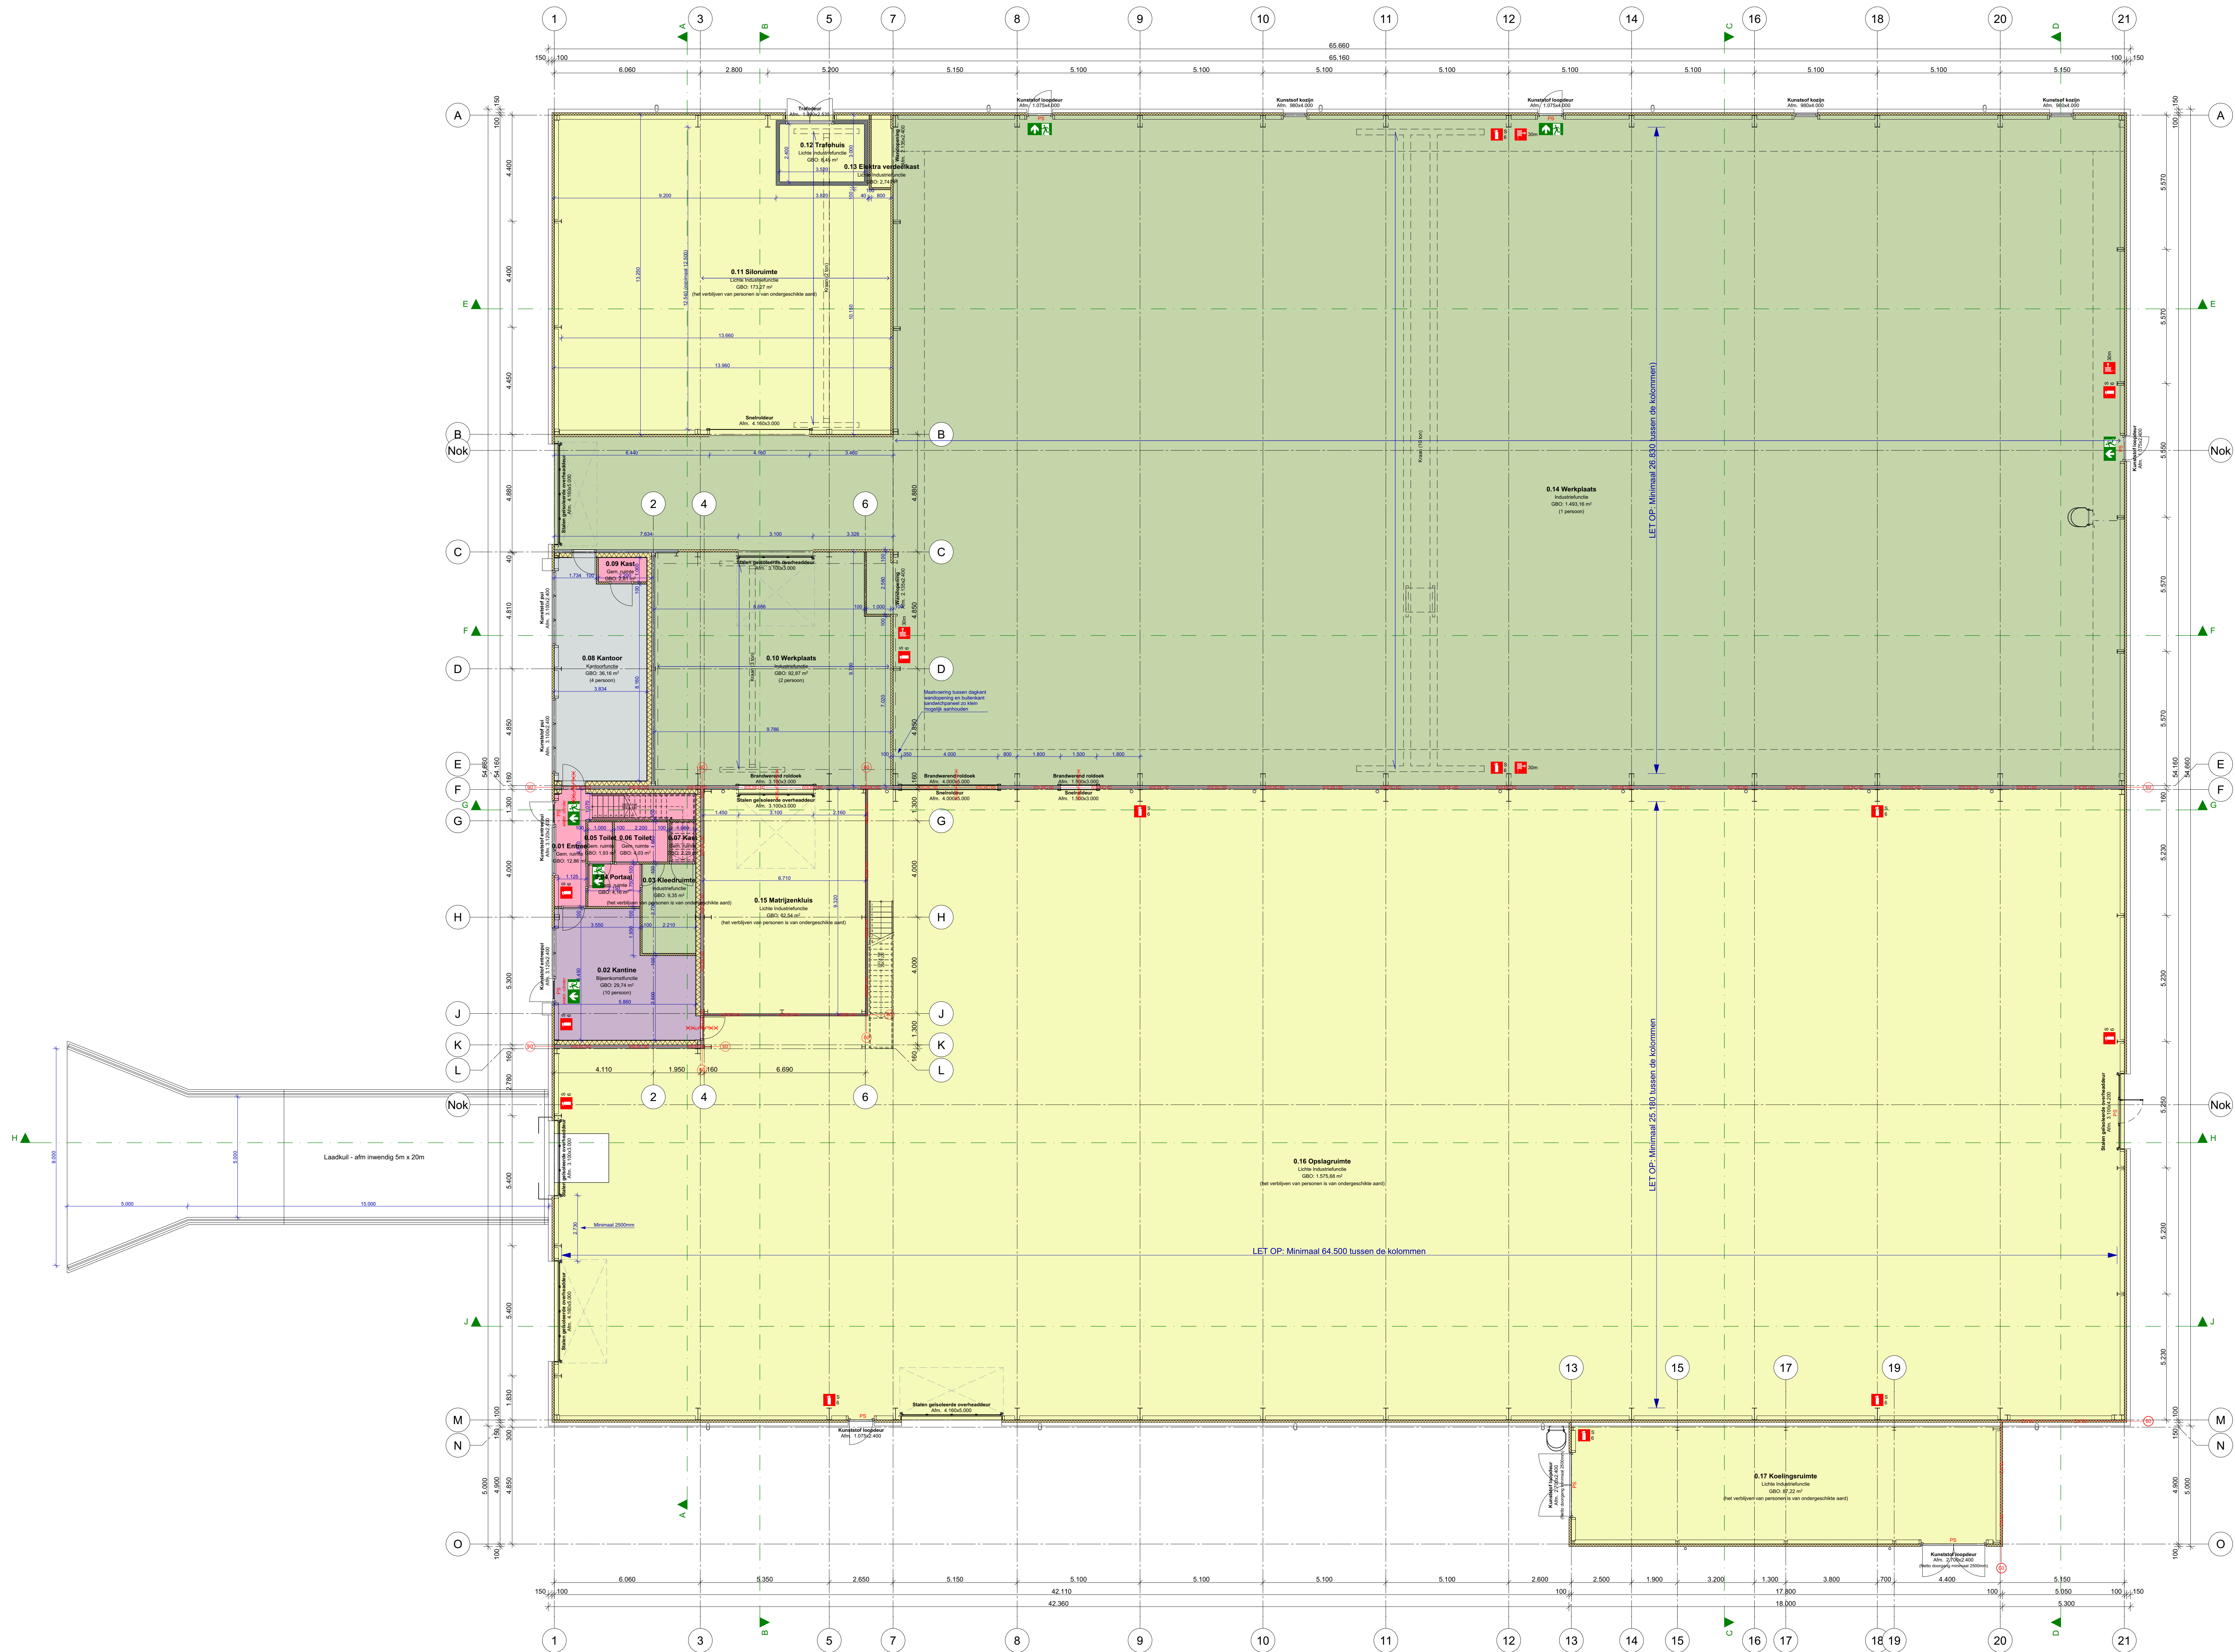

Deze tekening niet gebruiken voor uitvoering van enige werkzaamheden.
Staalconstructie- en funderingsberekeningen volgens opgaaf constructeur.
Bouwbesluittoetsing en BENG berekening volgens nader in te dienen rapportage

NEN-NORMERING:		VEILIGHEIDSMATREGELEN:	
Constructieve veiligheid:	NEN-EN 1993-1-1:1999	PS	Deur welke, over de minimaal vereiste breedte, zonder gebruik te maken van een sleutel, kan worden geopend. Dit is u.s. draaioverloop of gelijkaarsing
Brandbeveiliging vluchtweg:	NEN 13501-1	1	Vluchtweg aanduidingsbord / transparant verlichtingsarmatuur, uitvoering van de symbolen "UIT" en "NOODUITGANG" conform de pictogrammen zoals vermeld in de NEN 3871 / NEN-EN ISO 7010 en de zichtbaarheidsafstand conform de NEN-EN 1835.
Inbrandveiligheid:	NEN 5987/5096	1	Spootschuimblusser met een inhoud van ten minste 6 liter schuim.
Geluidsbescherming:	NEN 5077	1	Brandingsramp met een slanglengte van 30m
Vochtweringsgrenswaarde:	NEN 2778	1	Deur welke zwaartekracht is uitgevoerd, en in combinatie met het kozijn aan brandveiligheid bezit van ten minste 60 minuten (conform NEN 5096)
Afvoer vuilwater/hemelwater:	NEN 3215/7013	1	Deur welke zwaartekracht is uitgevoerd, en in combinatie met het kozijn aan brandveiligheid bezit van ten minste 60 minuten (conform NEN 5096)
Luchtverversing:	NEN 1087/8087	1	Deur welke zwaartekracht is uitgevoerd, en in combinatie met het kozijn aan brandveiligheid bezit van ten minste 60 minuten (conform NEN 5096)
Verbrandingsgasafvoer/ rookafvoer:	NEN 2767/6002	1	Deur welke zwaartekracht is uitgevoerd, en in combinatie met het kozijn aan brandveiligheid bezit van ten minste 60 minuten (conform NEN 5096)
Materialen:	NEN 2768	1	Deur welke zwaartekracht is uitgevoerd, en in combinatie met het kozijn aan brandveiligheid bezit van ten minste 60 minuten (conform NEN 5096)
Thermische isolatie:	NTA 8800	1	Deur welke zwaartekracht is uitgevoerd, en in combinatie met het kozijn aan brandveiligheid bezit van ten minste 60 minuten (conform NEN 5096)
Luchtdoorlatendheid:	NEN 2886	1	Deur welke zwaartekracht is uitgevoerd, en in combinatie met het kozijn aan brandveiligheid bezit van ten minste 60 minuten (conform NEN 5096)
Energieprestatie:	NTA 8800	1	Deur welke zwaartekracht is uitgevoerd, en in combinatie met het kozijn aan brandveiligheid bezit van ten minste 60 minuten (conform NEN 5096)
Drinkwater-installatie:	NEN 1006	1	Deur welke zwaartekracht is uitgevoerd, en in combinatie met het kozijn aan brandveiligheid bezit van ten minste 60 minuten (conform NEN 5096)
Electra-installatie:	NEN 1010/1041	1	Deur welke zwaartekracht is uitgevoerd, en in combinatie met het kozijn aan brandveiligheid bezit van ten minste 60 minuten (conform NEN 5096)
CV-installatie:	NEN 3026/1078	1	Deur welke zwaartekracht is uitgevoerd, en in combinatie met het kozijn aan brandveiligheid bezit van ten minste 60 minuten (conform NEN 5096)
INSTALLATIES:		INTERGRIEPE TOEGANGELIJKHEID:	
Alle installaties, zoals (rood)verlichting, water, riolering, enz. uitvoeren conform opgaaf en tekeningen van installateur.		De vrije doorgang van alle toegangen tot ruimtes dient minimaal 180x2100mm te zijn, conform BBL art. 4.102 lid 1. (Daarbij is de opstaphoogte bij entree deuren niet groter dan 20mm, conform BBL art. 4.102 lid 5)	
WERING MUZEN EN RATTEN:		MATERIALIEN EN KLEUREN:	
Opvoering in fundering: voor de de wand zijn "muurplaat" (conform BBL art. 4.144 en 4.145)		De aanwezigheid en uitvoering van een brandveiligheidsinstallatie voldoet minimaal aan de in BBL art. 4.206 gestelde voorwaarden (bepaald conform NEN 2535)	
GEBOUWGEVEENS:		GEBOUWGEVEENS:	
Rebouwd oppervlakte: GBO / VG GRO+GR: 3078m²		Rebouwd oppervlakte: GBO / VG GRO+GR: 3078m²	
Bruto inhoud: 34689m³		Bruto inhoud: 34689m³	
Gem. ruime (GR): 38.5m²		Gem. ruime (GR): 38.5m²	
GBO Lichte ind. functie: 2327.4m²		GBO Lichte ind. functie: 2327.4m²	
VG Lichte ind. functie: 1595.4m²		VG Lichte ind. functie: 1595.4m²	
GBO Industriële functie: 1595.4m²		GBO Industriële functie: 1595.4m²	
VG Industriële functie: 1595.4m²		VG Industriële functie: 1595.4m²	
GBO Kantoorfunctie: 74.3m²		GBO Kantoorfunctie: 74.3m²	
VG Kantoorfunctie: 74.3m²		VG Kantoorfunctie: 74.3m²	
GBO Bijkantoorfunctie: 49.3m²		GBO Bijkantoorfunctie: 49.3m²	
VG Bijkantoorfunctie: 49.3m²		VG Bijkantoorfunctie: 49.3m²	
GBO Opslagruimte: 49.3m²		GBO Opslagruimte: 49.3m²	
VG Opslagruimte: 49.3m²		VG Opslagruimte: 49.3m²	
MATERIALIEN EN KLEUREN:		MATERIALIEN EN KLEUREN:	
Ondergrond: Materiaal: Kleur: Kleurcode:		Ondergrond: Materiaal: Kleur: Kleurcode:	
Dak: Dak: Kleur: Kleurcode:		Dak: Dak: Kleur: Kleurcode:	
Wanden: Wanden: Kleur: Kleurcode:		Wanden: Wanden: Kleur: Kleurcode:	
Afbekleding: Afbekleding: Kleur: Kleurcode:		Afbekleding: Afbekleding: Kleur: Kleurcode:	
Borstelwerk: Borstelwerk: Kleur: Kleurcode:		Borstelwerk: Borstelwerk: Kleur: Kleurcode:	
Korven: Korven: Kleur: Kleurcode:		Korven: Korven: Kleur: Kleurcode:	
Overbreek: Overbreek: Kleur: Kleurcode:		Overbreek: Overbreek: Kleur: Kleurcode:	
Galen: Galen: Kleur: Kleurcode:		Galen: Galen: Kleur: Kleurcode:	

Opdrachtgever: Logistiek Beheer B.V.
Waalsteeg 124
7345 CG Wierum Wiesel

Tekenaar: NVV
Datum: 07 maart 2025
Schaal: 1:100
Formaat: A0




Wijziging: 01
Wijziging: 02
Postbus 378
3900 AJ VEENDAALE
www.hardeman.nl
info@hardeman.nl

T: 0318 - 521700
F: 0318 - 520418
E: info@hardeman.nl

Werknummer: 44449
Bidsnummer: 3



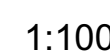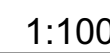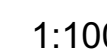

NEN-NORMERING: VEILIGHEIDSMATREGELEN:

VEILIGHEIDSMATREGELEN:

"karnielconstructie", WBDO = 60 minuten o.b.v. spiegelsymmetrie.

Een zijde van een constructieonderdeel die grenst aan de buitenlucht voldoet min aan de in BBL art.4.44 gestelde brandklasse (bepaald conform NEN-EN13501-1).

De weerstand tegen rookdoorgang voldoet minimaal aan de in BBL art. 4.61 en art. 4.62 gestelde eisen (bepaald conform NEN 6075).

De aanwezigheid en uitvoering van een brandmeldinstallatie voldoet minimaal aan de BBL art. 4.208 gestelde voorschriften (bepaald conform NEN 2535).

De aanwezigheid en uitvoering van een ontruimingsinstallatie voldoet minimaal aan BBL art 4.213 gestelde voorschriften (bepaald conform NEN 2575).

MATERIALEN EN KLEUREN:

Dak:	Staal / PVC	Lichtprijs	RAL 7038 / N
------	-------------	------------	--------------

Wanden:	Staal	Grismetallic	RAL 9007
Accentvlakken:	Staal	Antraciet	RAL 7016

Strijpsplint	Aluminium	Anticracl	RAL 7016
Borstwering:	Beton	Grijs	N.v.t.
Korrelen:	Kunststof	Anticracl	RAL 7016

Deuren / Ramen:	Kunststof	Antraciet	RAL 7016
Overheaddeuren:	Staal	Antraciet	RAL 7016
Opbouwdeuren:	Staal	Antraciet	RAL 7016

HARDEMA


Format: A0

Wijziging: Postbus 378 T: 0318 - 52170
Wijziging: 0318 - 52170

Wijziging: Generatorstraat 21 I: www.hardem
Wijziging: 3903 LH VEENENDAAL E: info@hardem
Wijziging:




336 • JOURNAL OF POST KEYNESIAN ECONOMICS • Volume 14 Number 3

11149 6

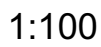

NEN-NORMERING: VEILIGHEIDSMATREGELEN:



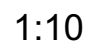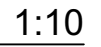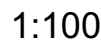

NEN-NORMERING: _____

INSTALLATIES:

Alle installaties, zoals (nood)verlichting, water, riolering, enz. uitvoeren conform opgaaf en tekeningen van installateur.

Uitzondering daarop is de bovenzijde van het dak (uitvoering conform BBL art. 4.4).

WERING MUIZEN EN RATTEN:

GEBOUWGEGEVENS: De aanwezigheid en uitvoering van een entruimingsinstallatie voldoet minimaal aan BBL art 4.213 gestelde voorschriften (bepaald conform NEN 2575).

Bruto inhoud:	34689m³	Onderdeel:	Materiaal:	Kleur:	Kleurcode:
		Dak:	Staal / PVC	Lichtroos	RAL 7008 / N

GBO Industriefunctie:	1595,4m ²	1610,6m ²	Stienlsten:	Aluminium	Anticrict	RAL 7016
VG Industriefunctie:	1595,4m ²		Borstwering:	Beton	Grips	N.v.t.
GBO Kantoorfunctie:	74,2m ²	74,2m ²				RAL 7016

VG B-jeerkonstrunctie:	48,9m	Goten / H.w.a.'s:	Aluminium / PVC	Grijs / Grijs	RAL 7036 / N
------------------------	-------	-------------------	-----------------	---------------	--------------

Logvast Beheer B.V.
Wieselsweg 124
7345 CG Marum (Wissel)

Schaal: 1:100, 1:10
Formaat: A0

 **HARDEMA**
VEENEND.

Herlog van Beijerenstraat 2
2461 EM Ter Aar

Onderwerp:	Werknummer:	Bladnummer:
B... ..	11112	2