
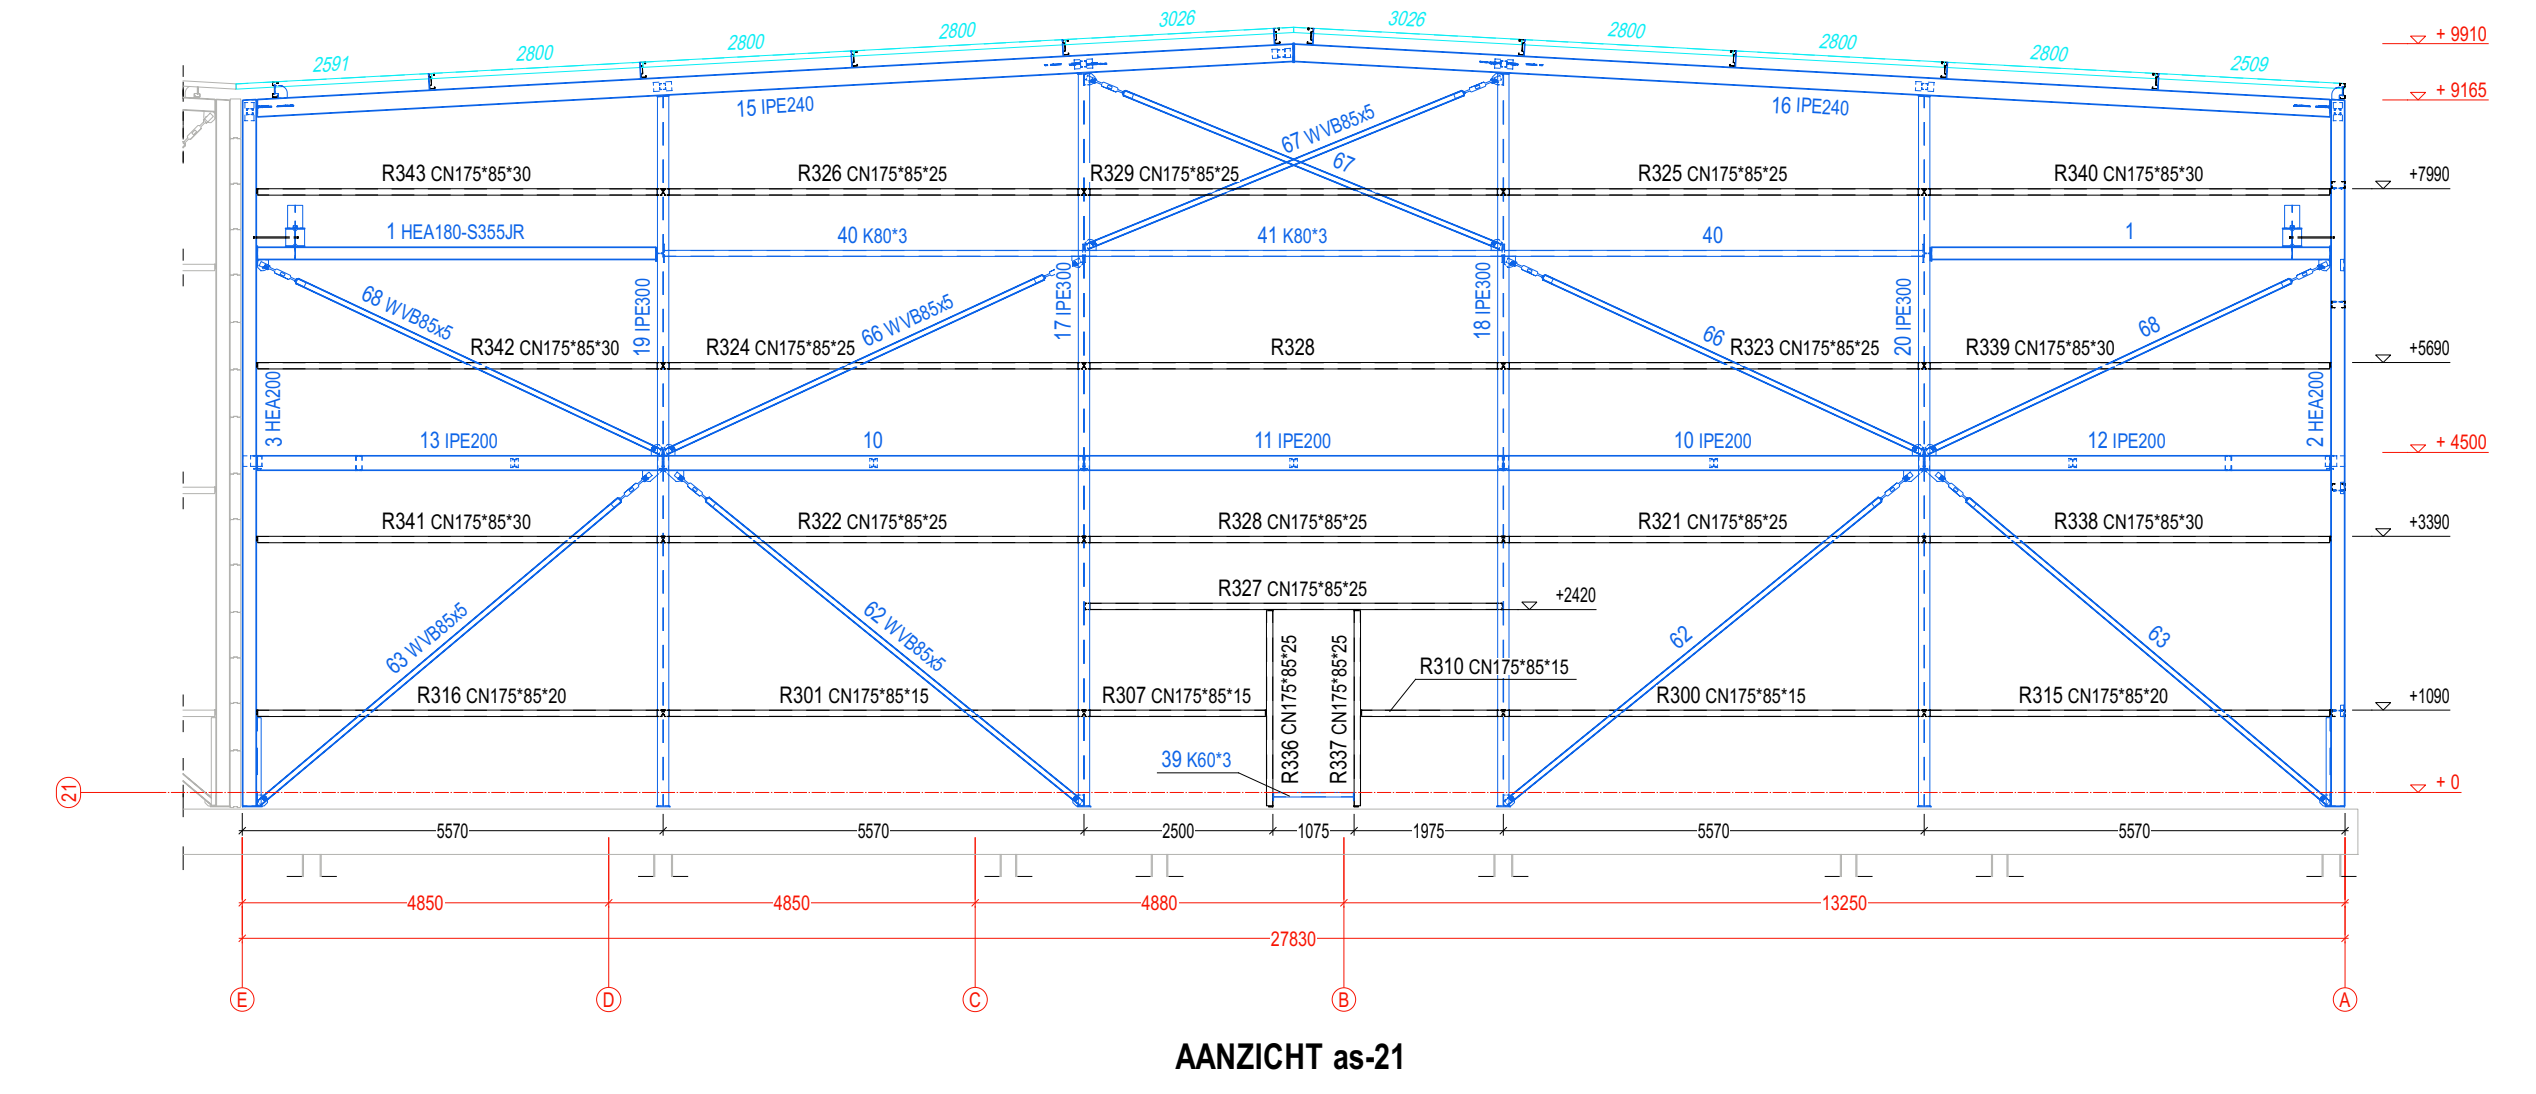
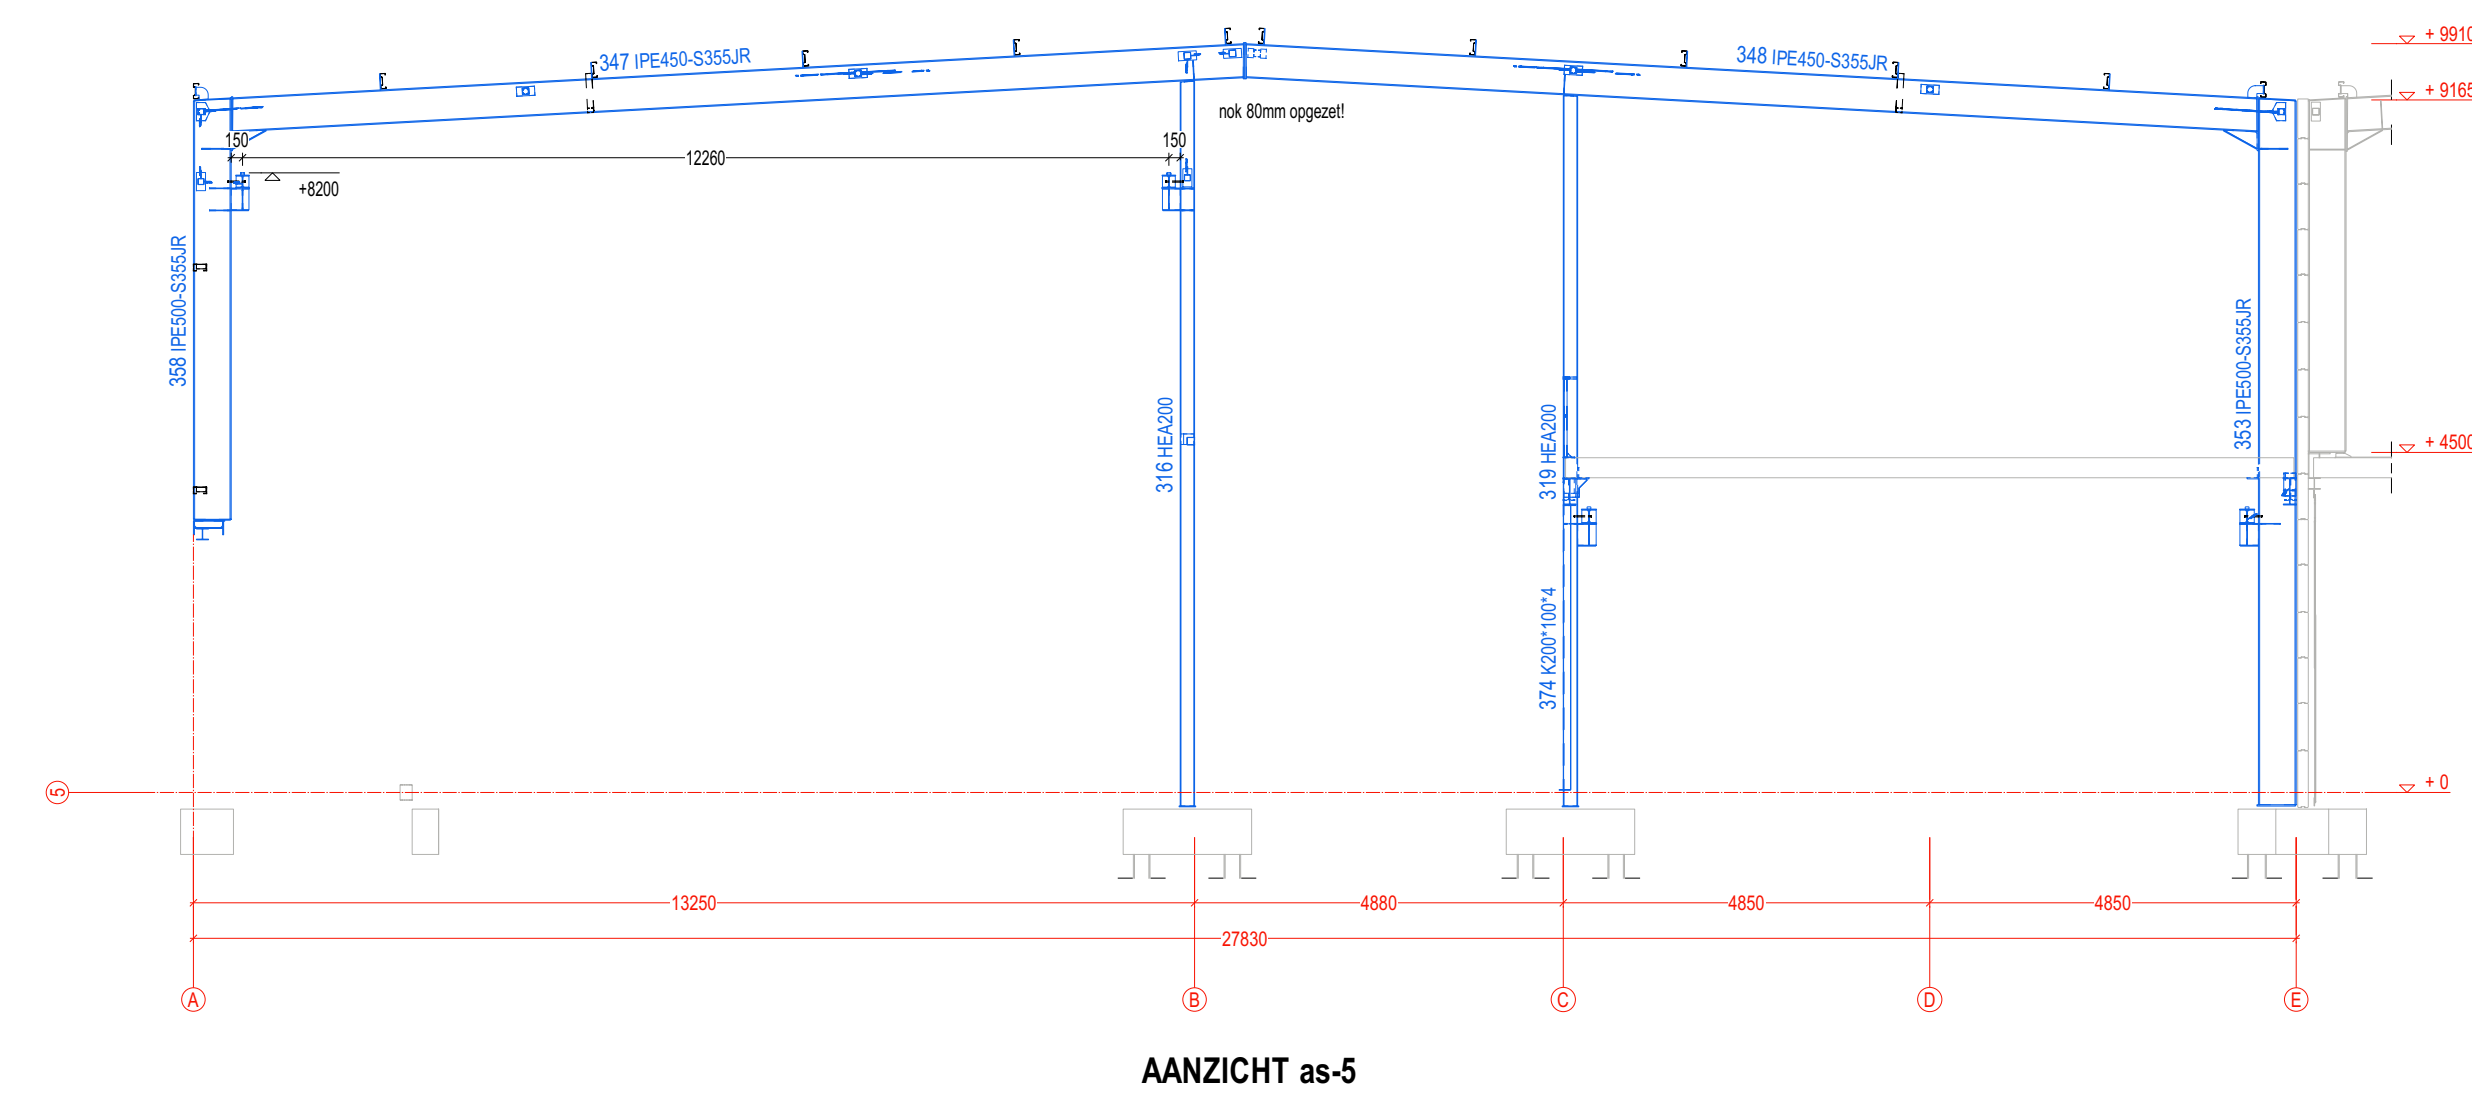
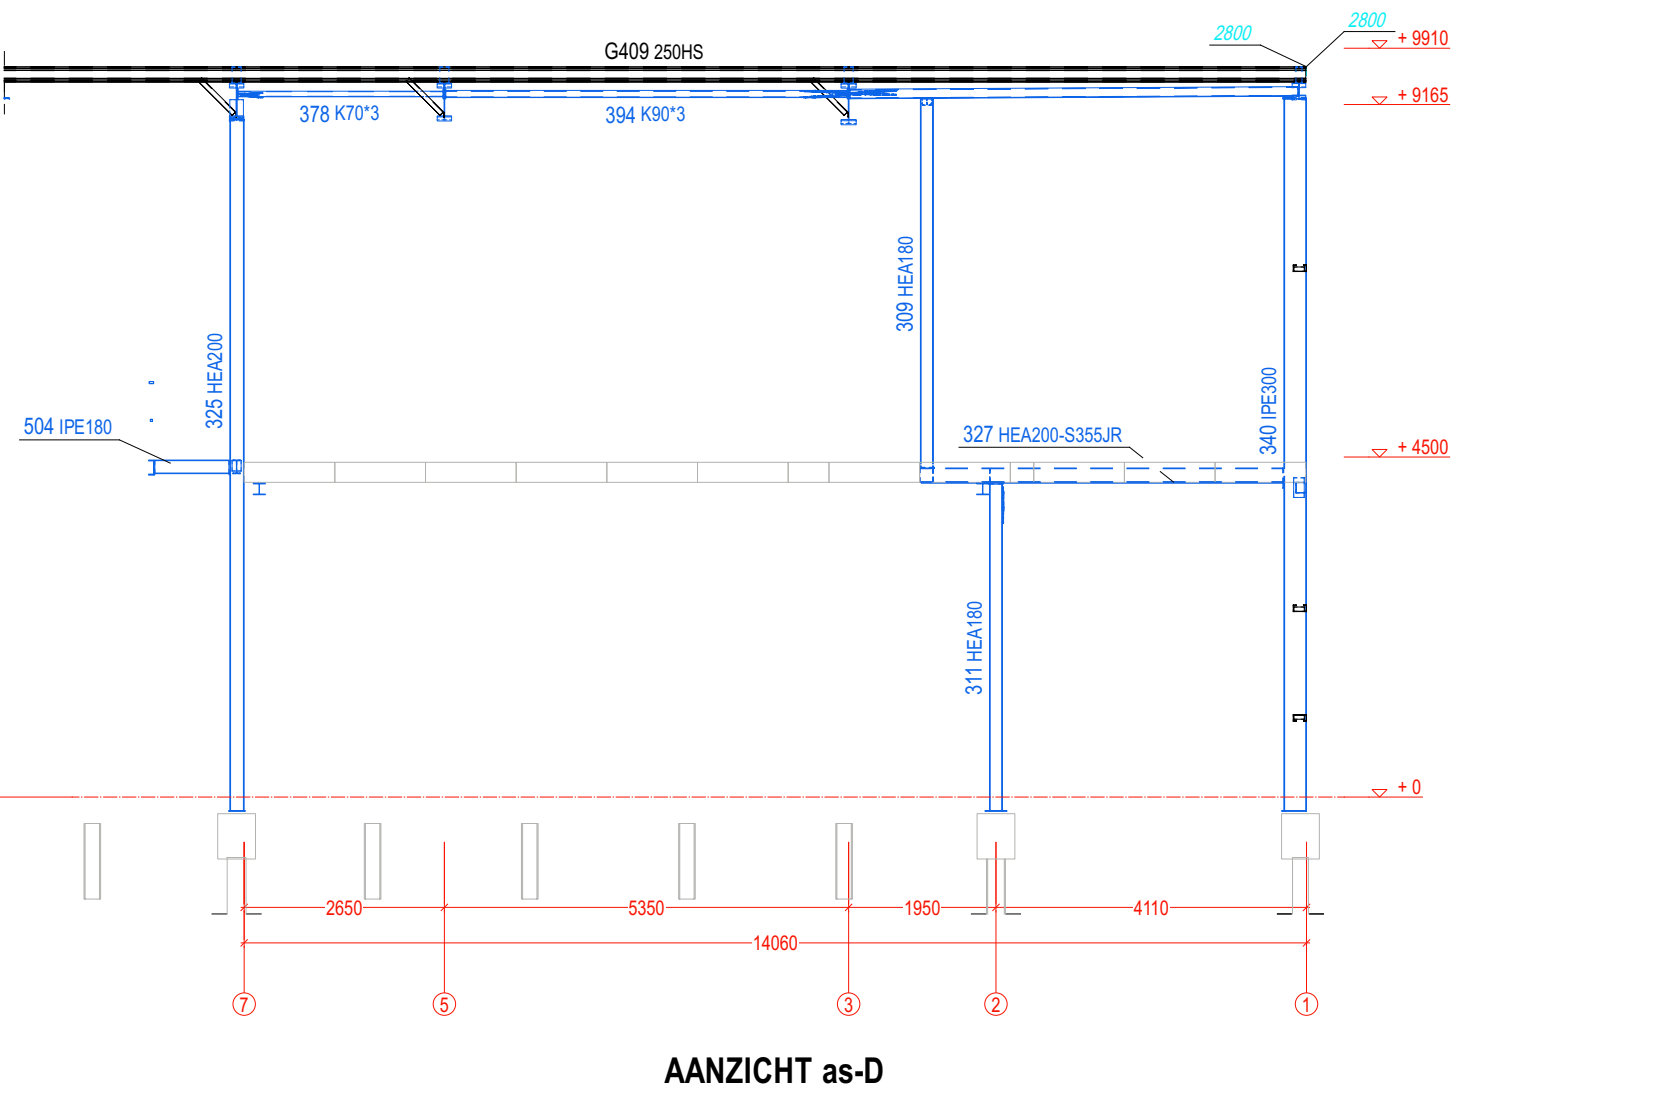
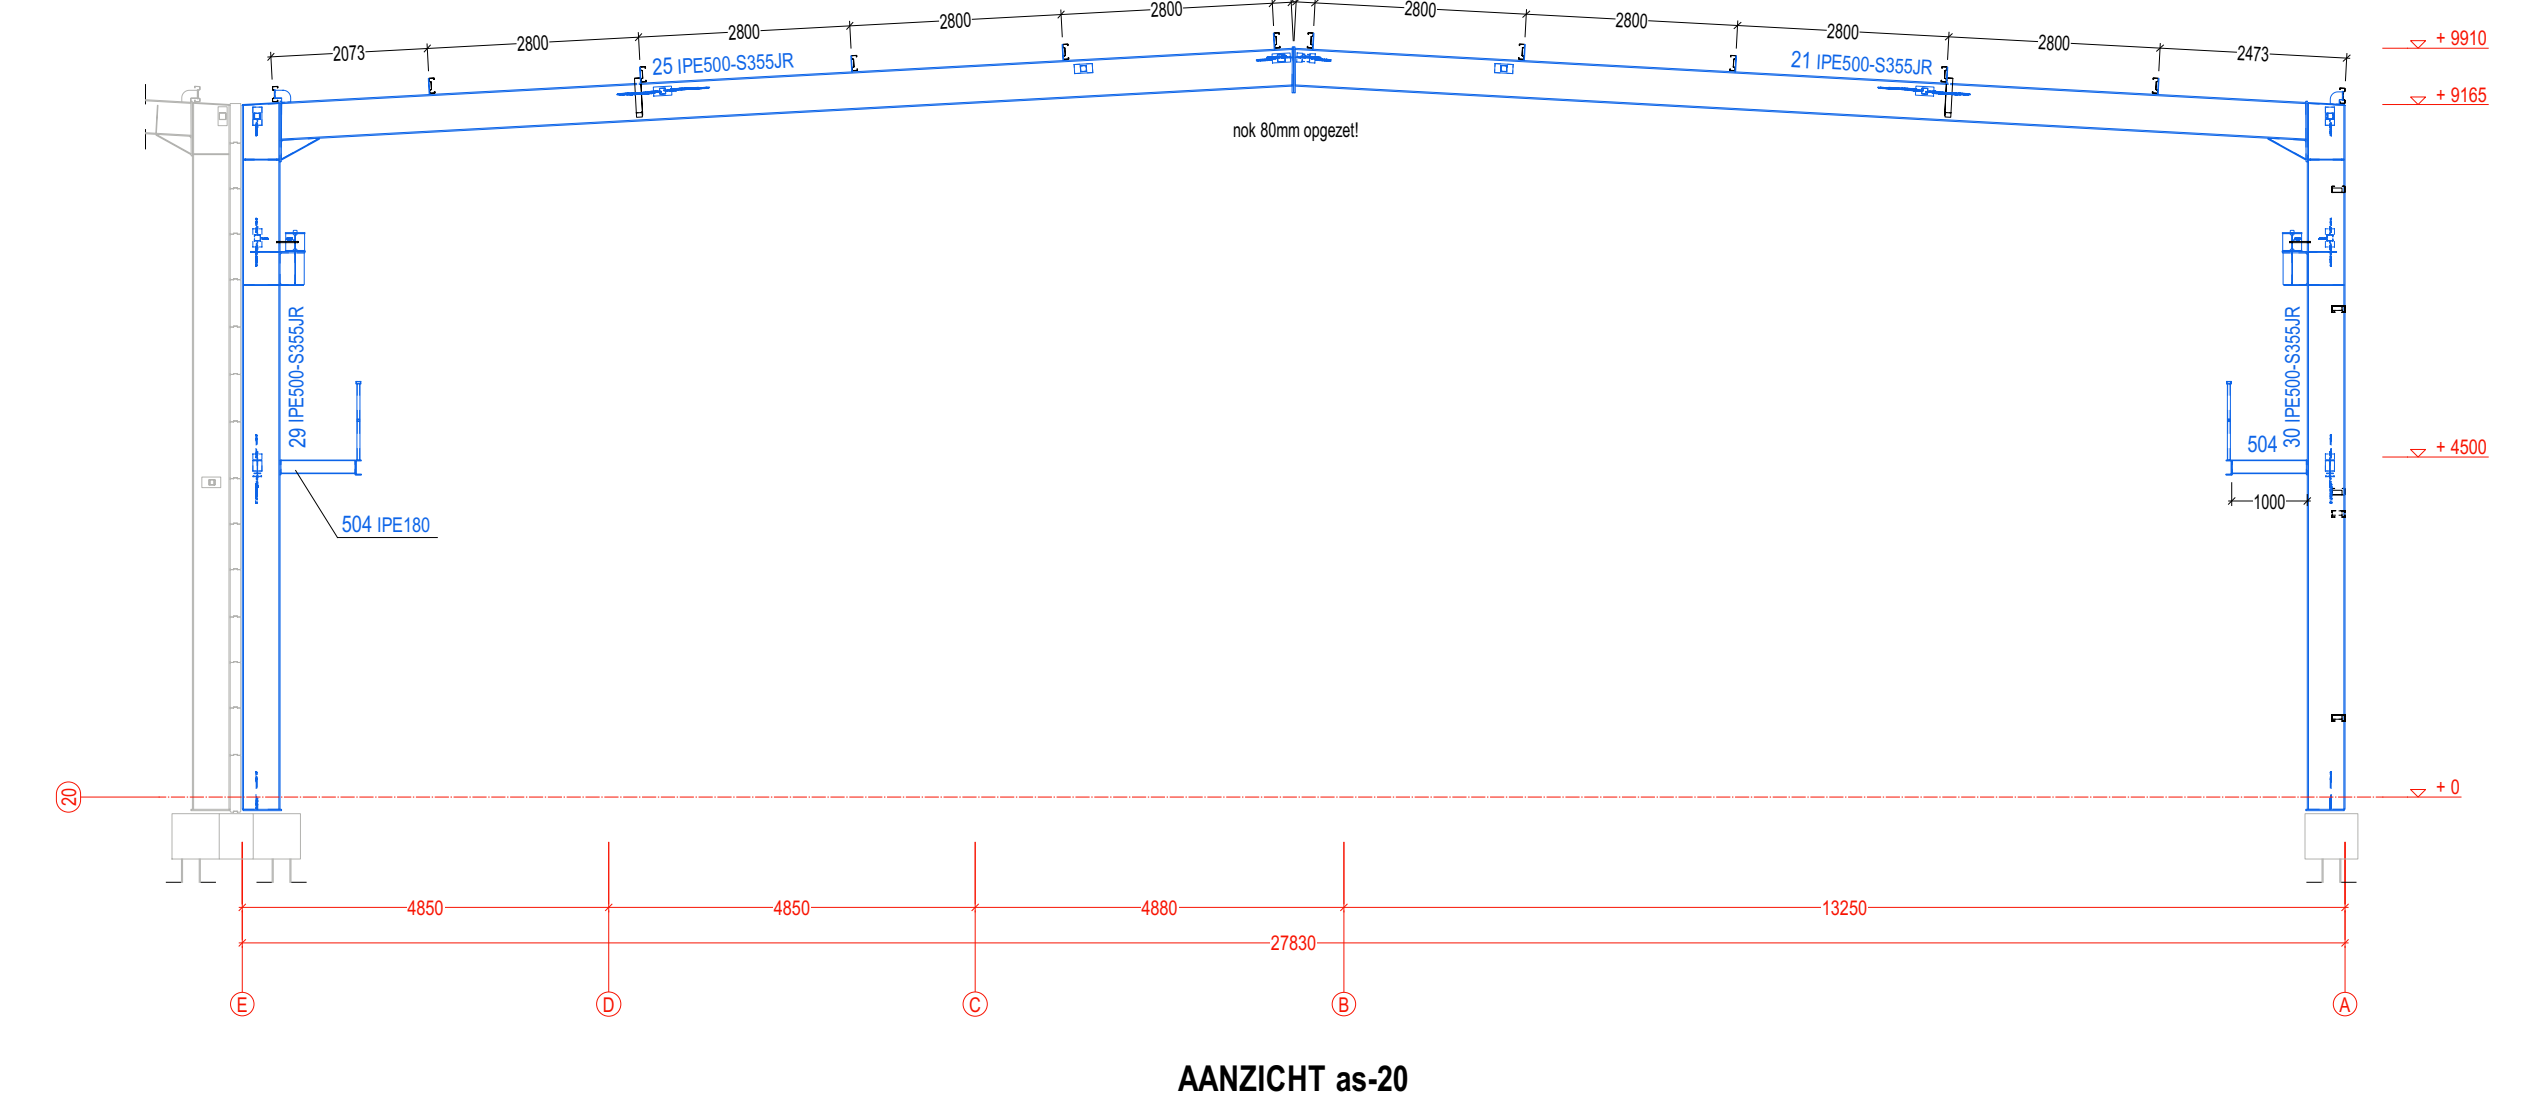
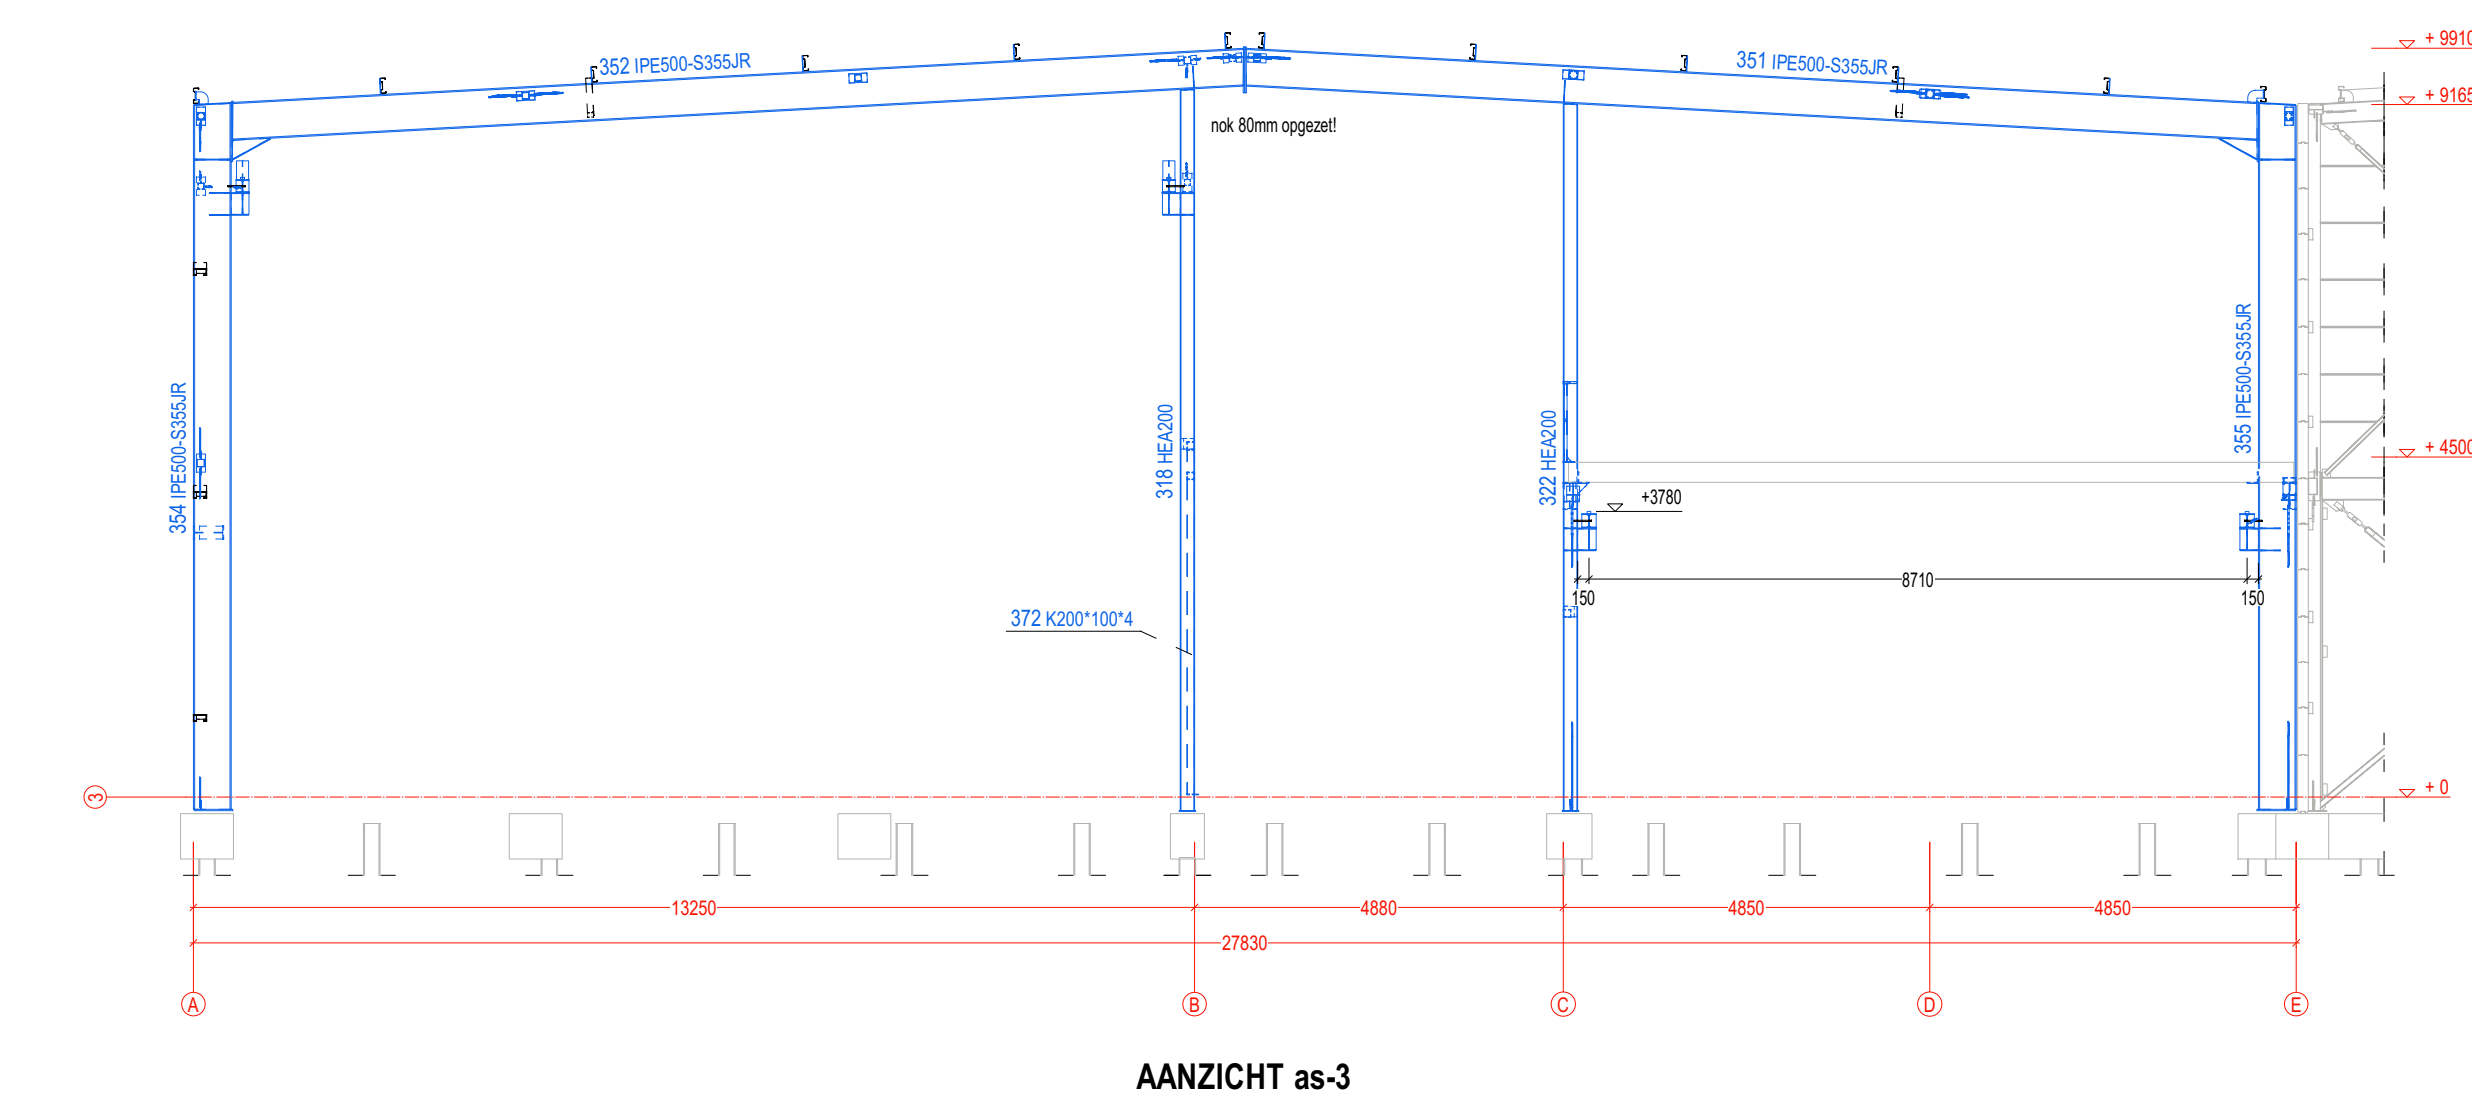
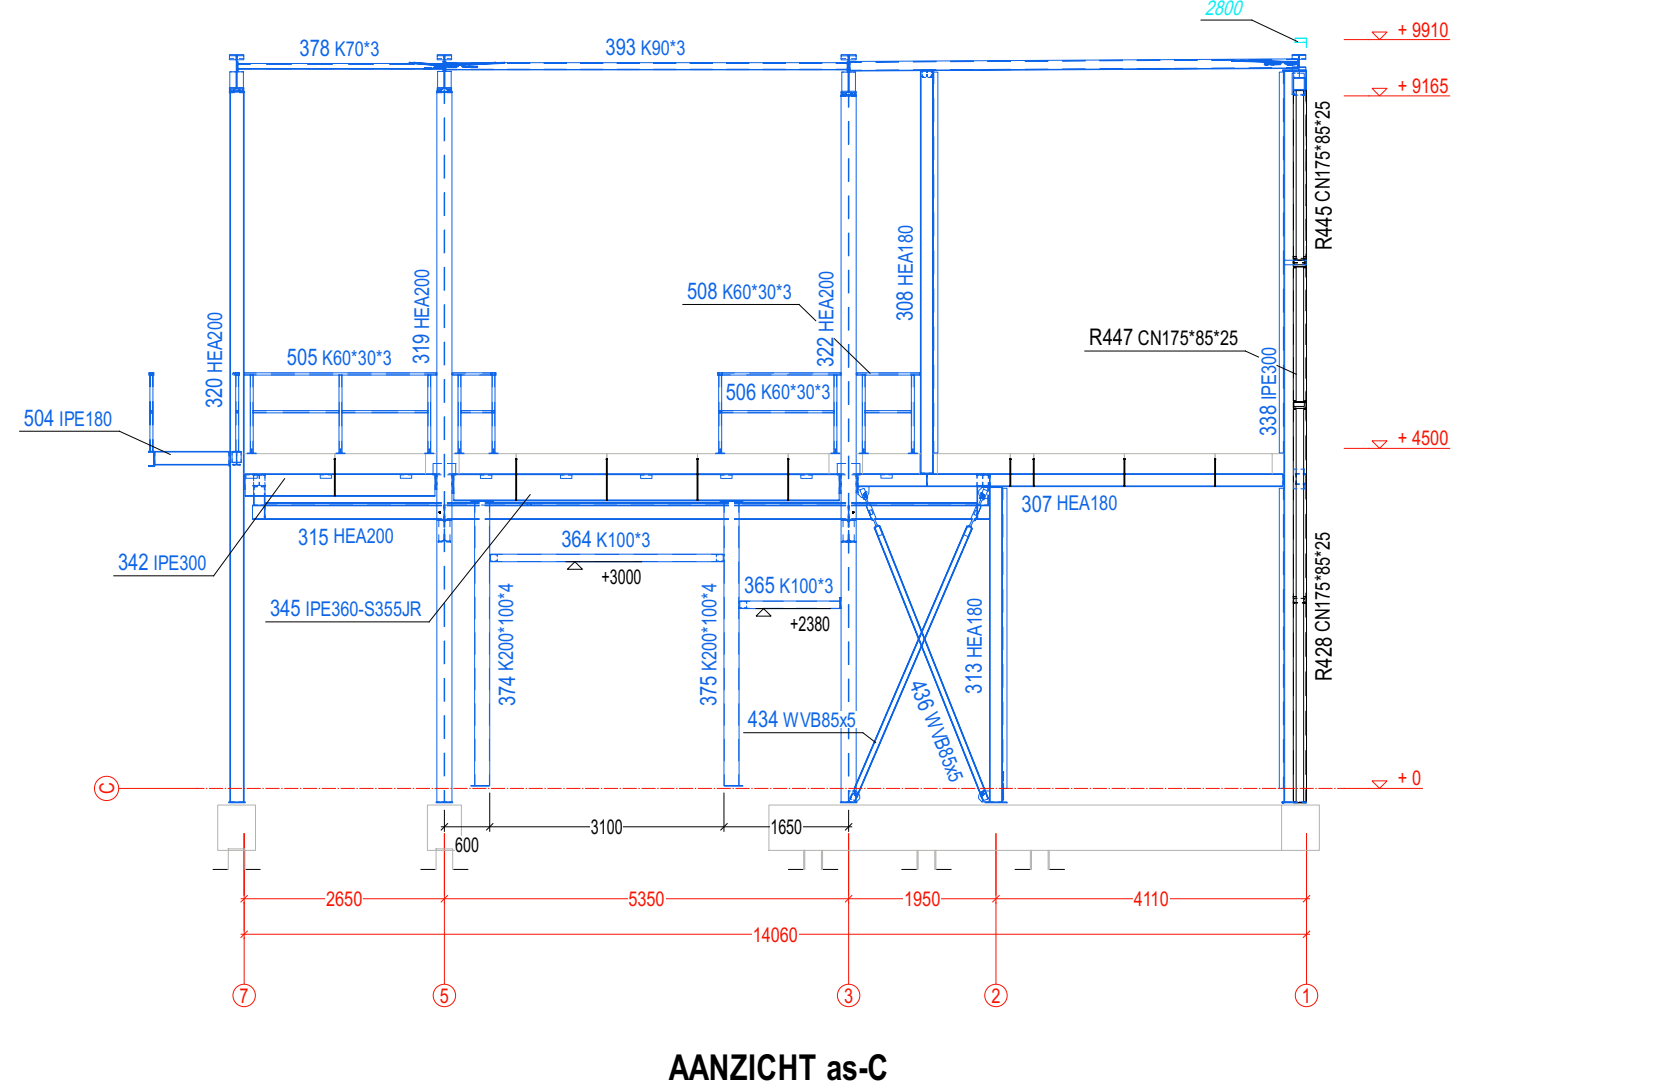
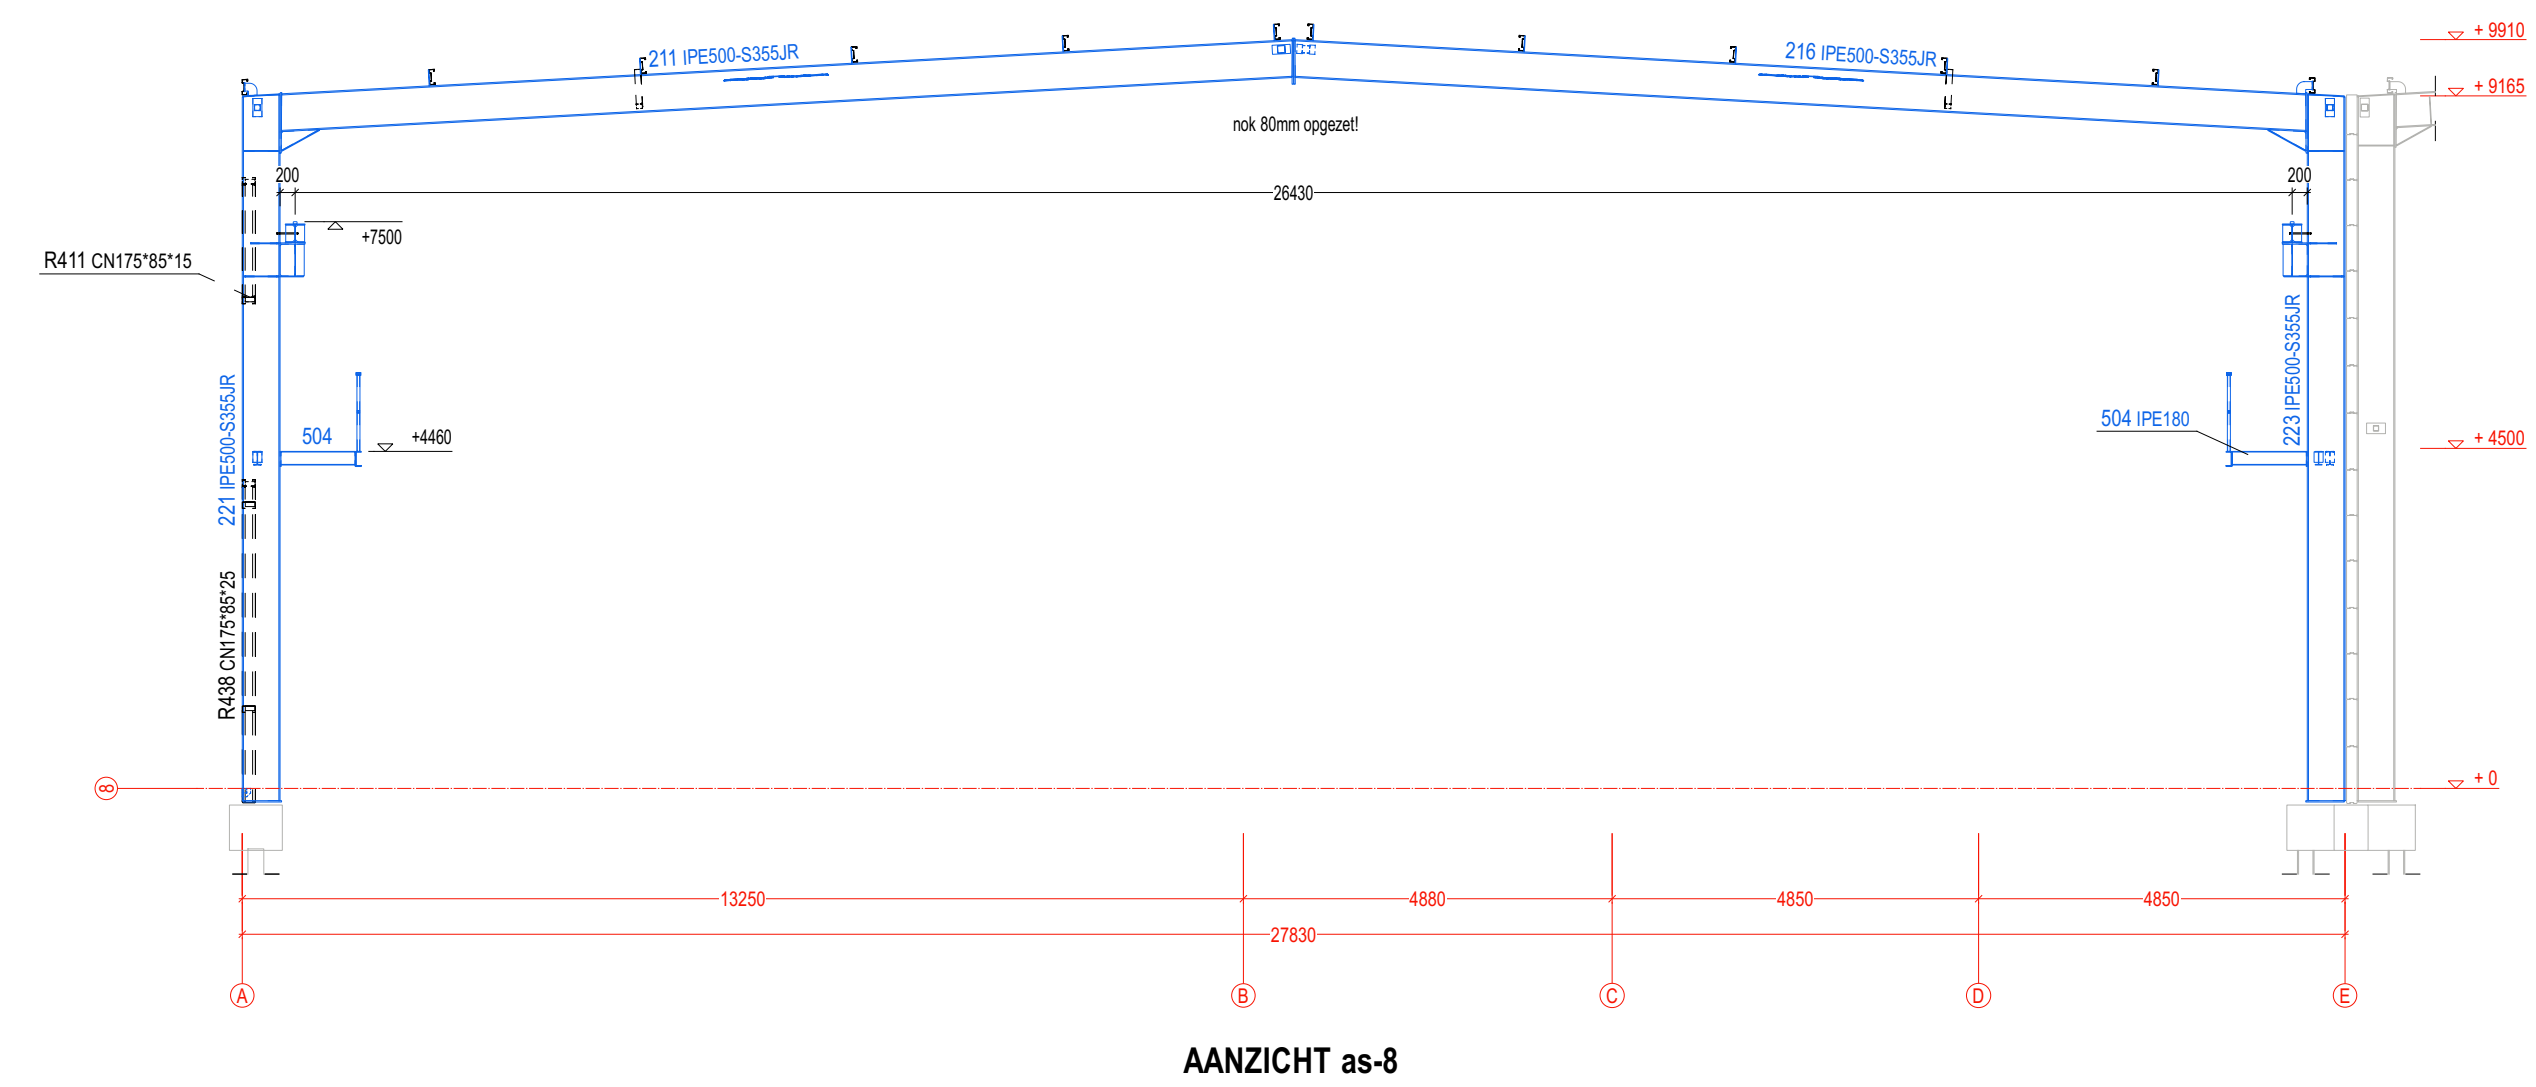
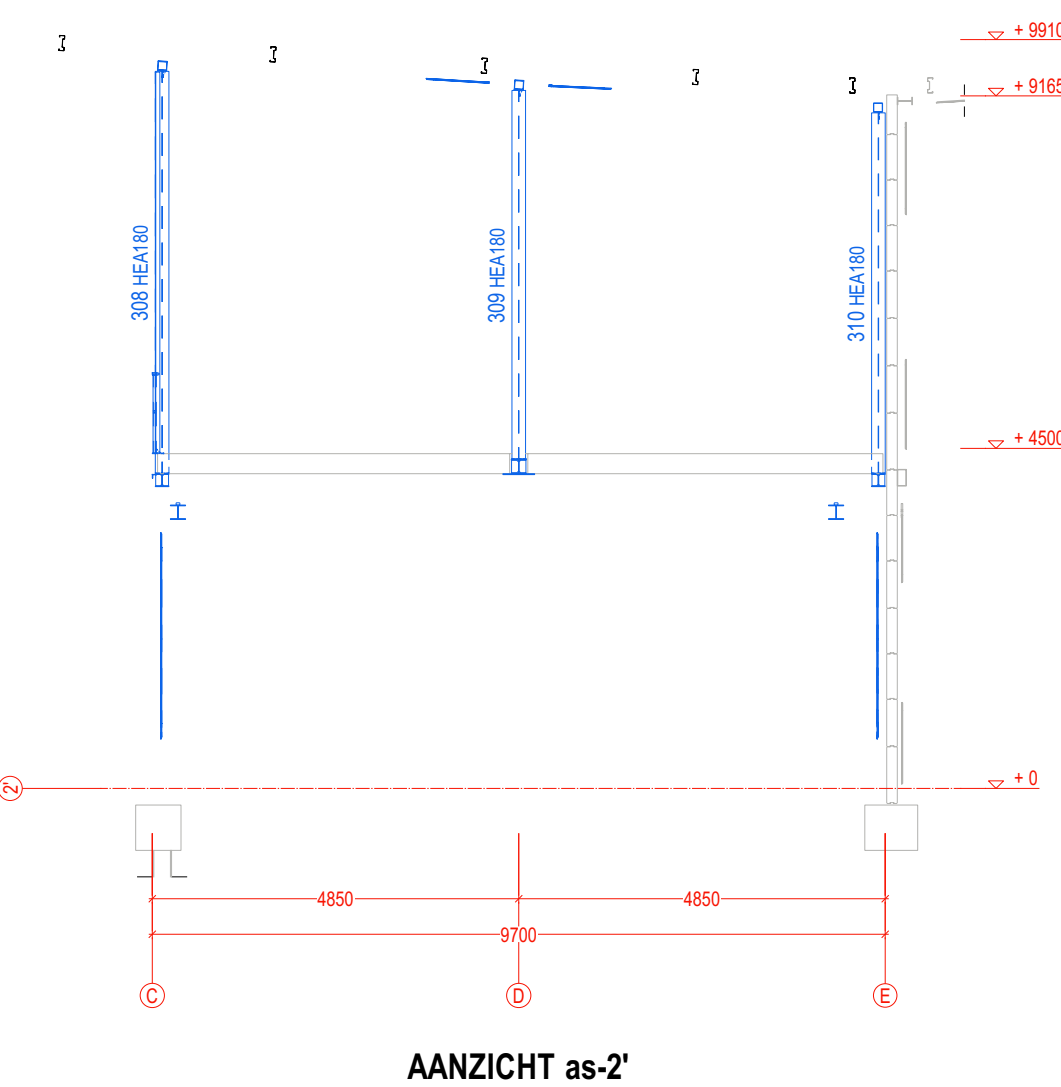
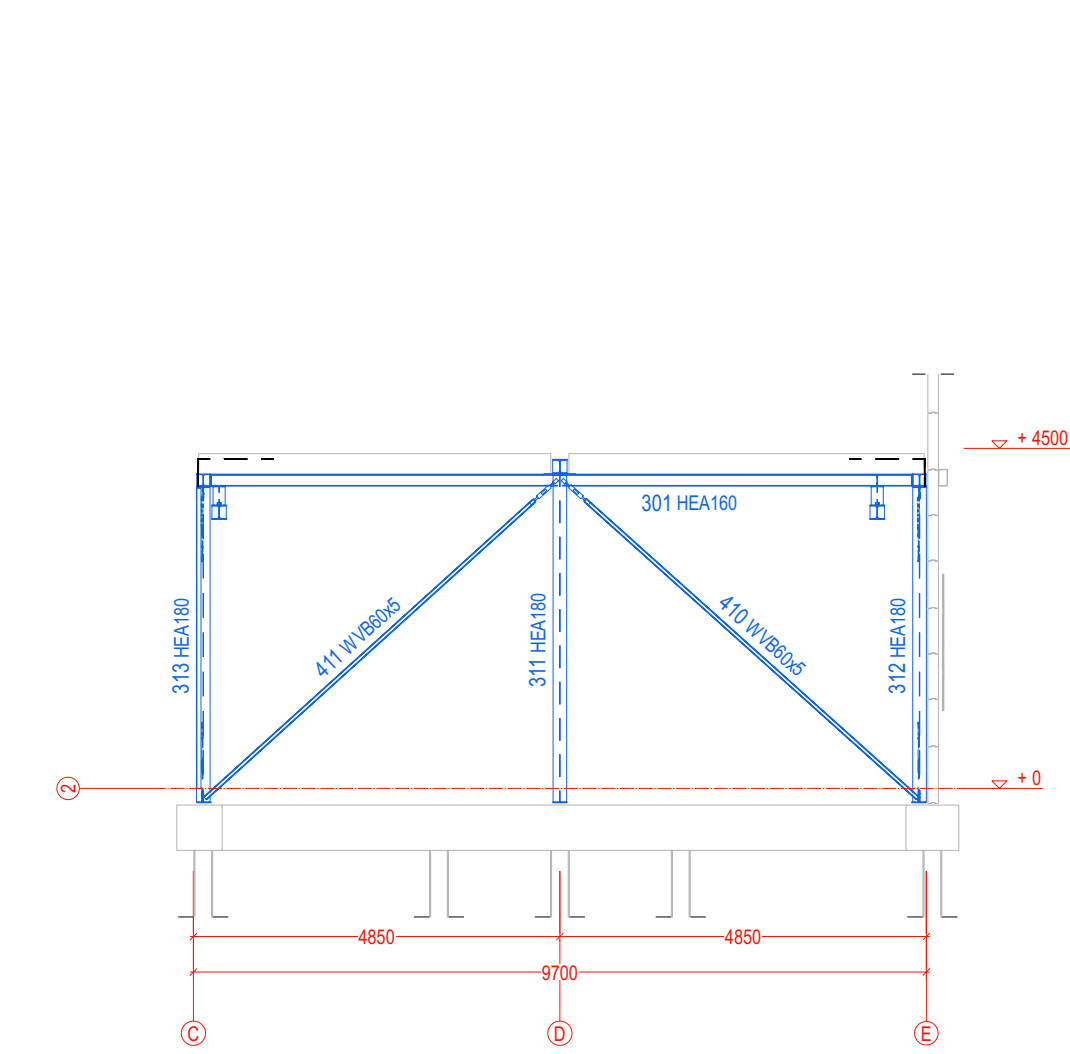
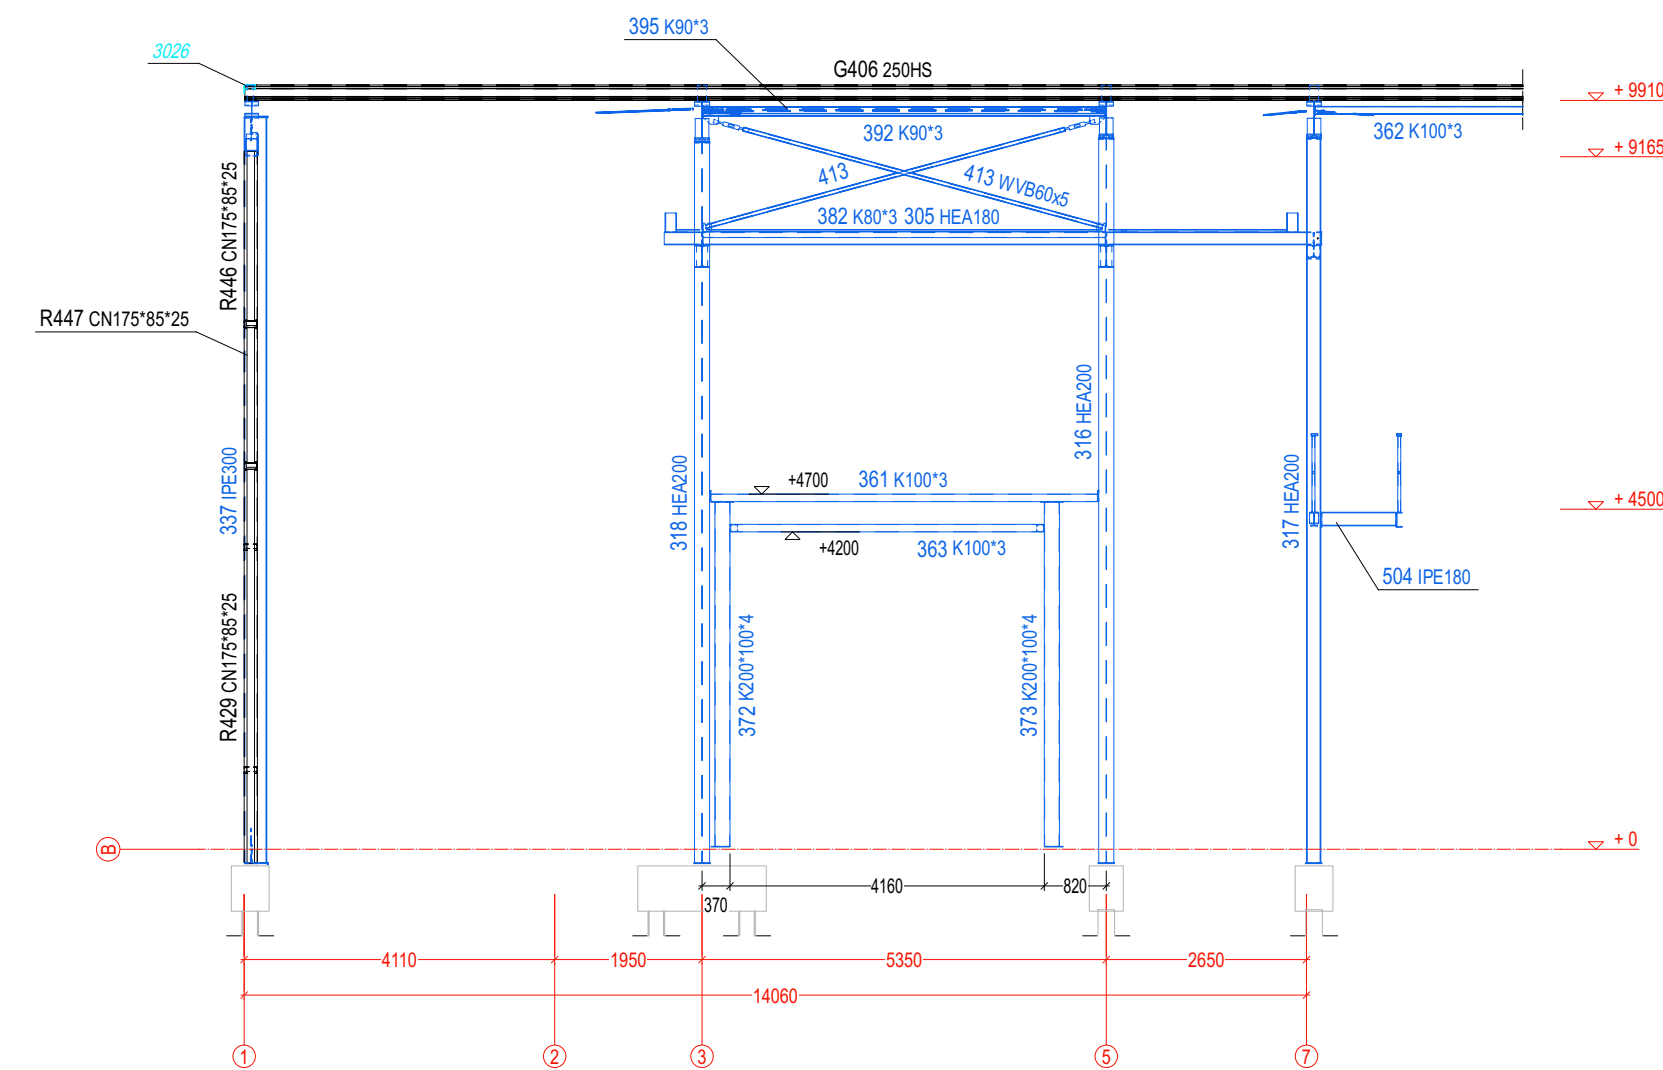
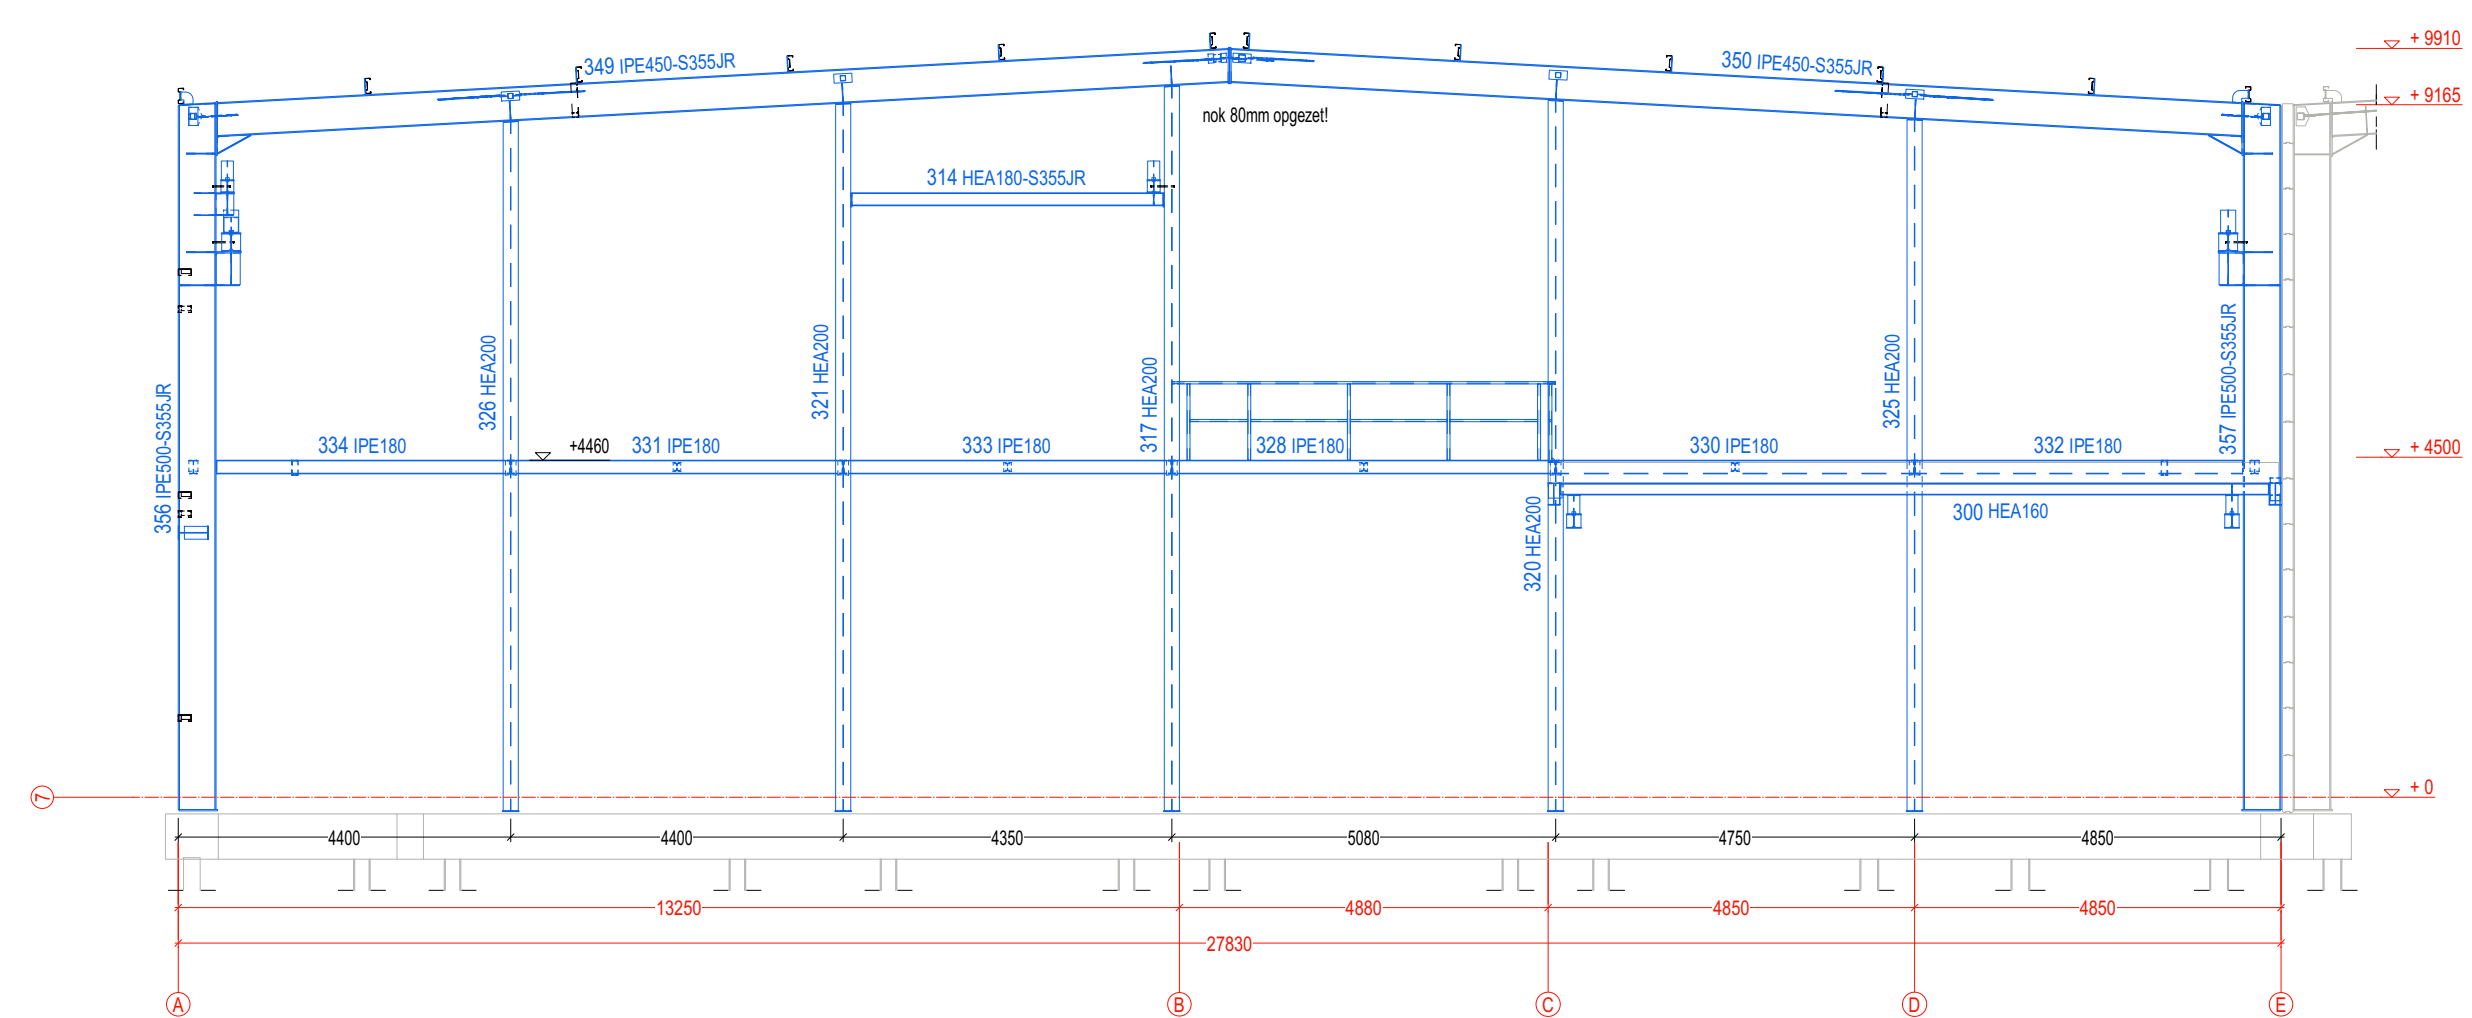


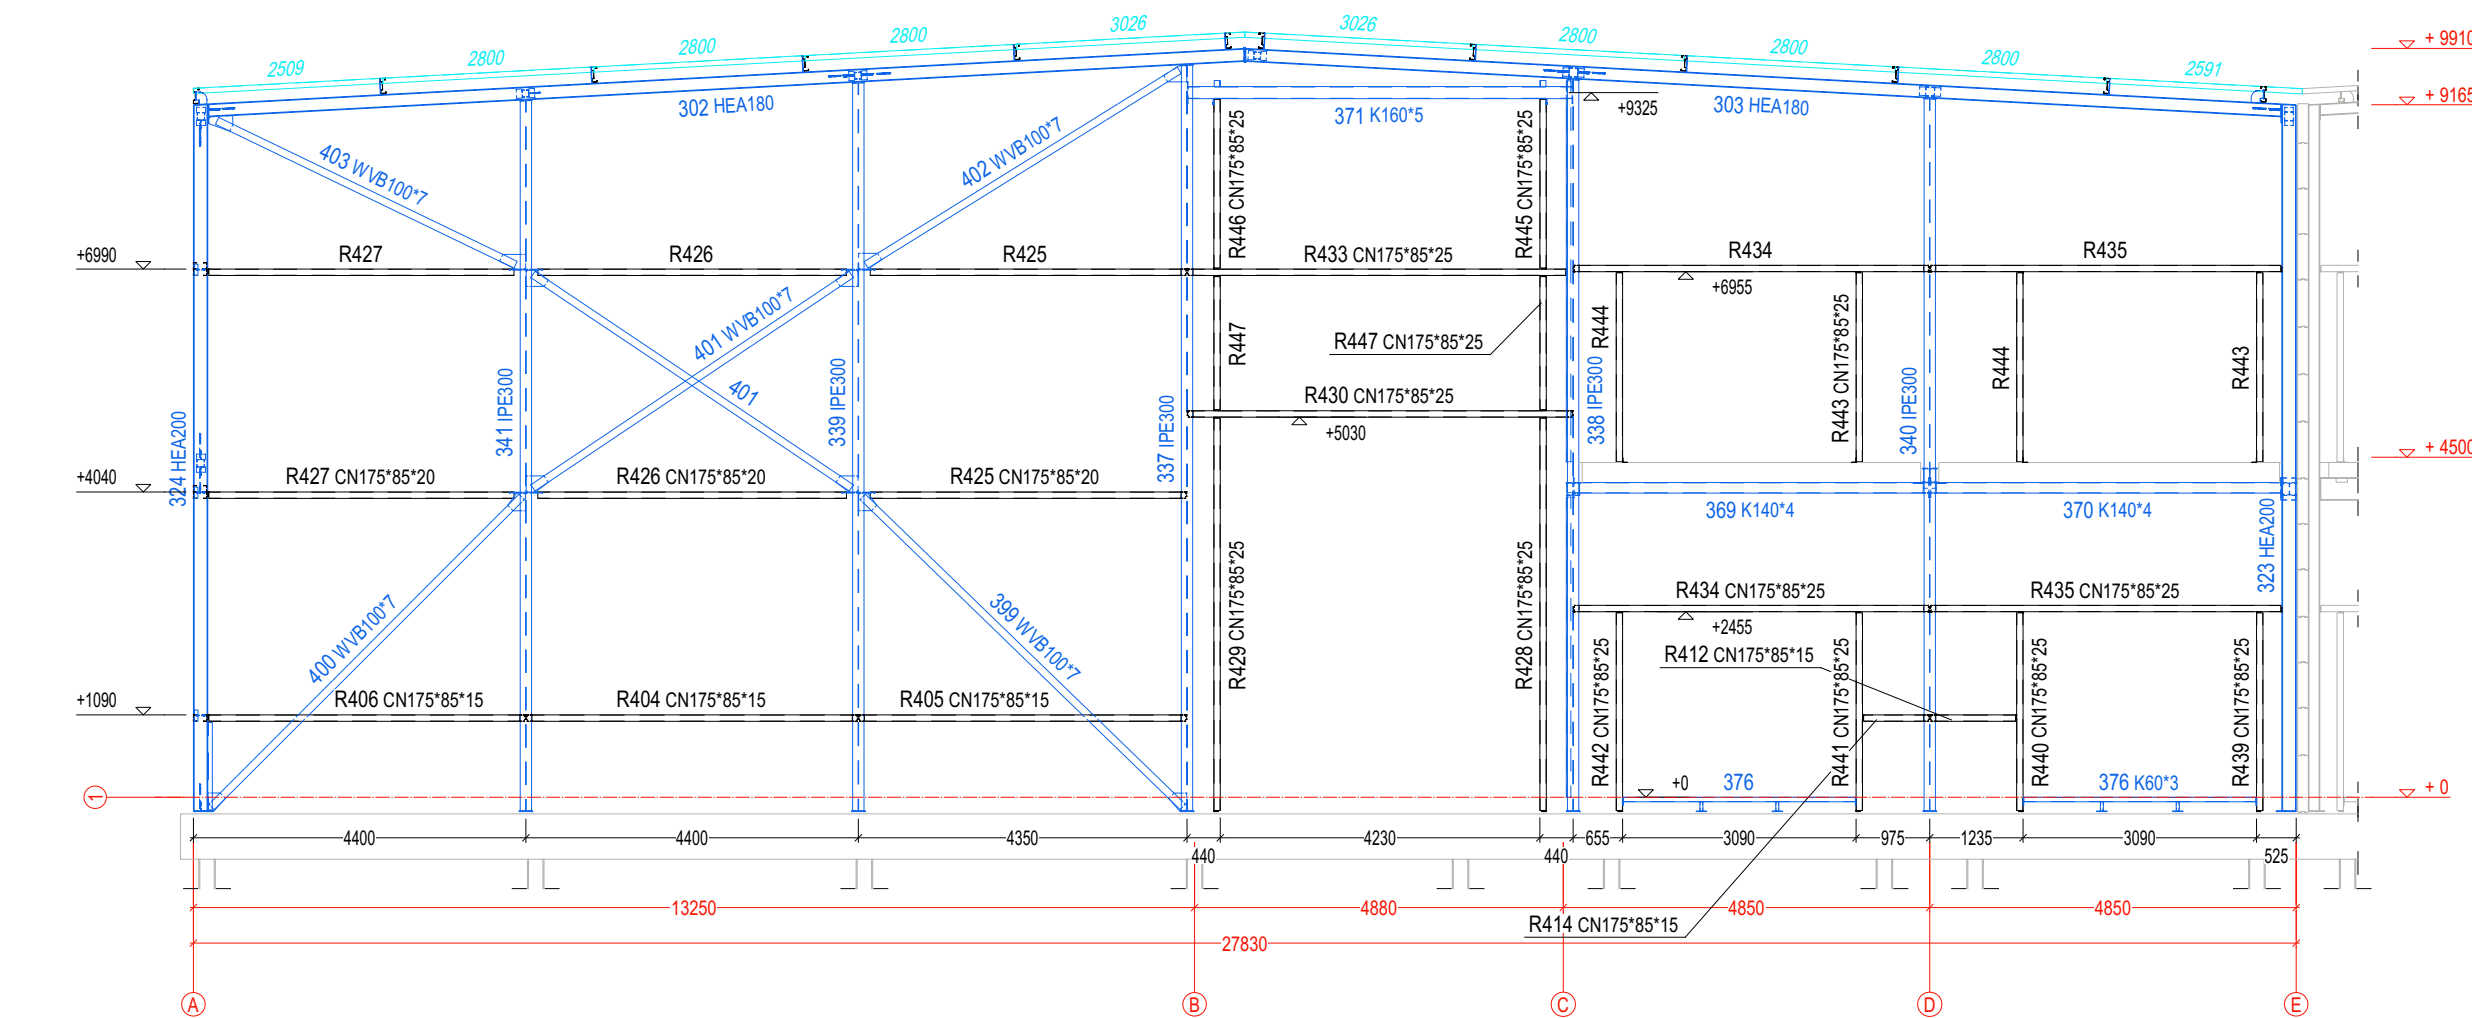

Staalwalfact	Behandeling
wb 60x85x100z	S-500GD
kokers/buizen	S-235 1x102 anders aangeven
overig staal	S-235 1x102 anders aangeven
bouten/moeren	8.8
	staalconstructie
	1-lagige poedercoating 60µm RAL... ??
	wb 50x55x5
	verzinkt
	Sendzimir verzinkt
	gordingen
	Sendzimir verzinkt
	wandregels

Overige	
wandregels	C175x65 , dikte 1.52/02.53.0mm
deursteelen as-1	C300x60 , dikte 2.9mm
kanaalplaten	dikte 200/265mm
deklaag	gewapende druklaag dikte 70mm (enkelnet ø5-150)
-	-

	E	-
	D	+
	C	+
	B	+
	A	+
Wijzing	Index	Datum

Opdrachtgever Logivast Beheer BV	Status: TER CONTROLE	Telefoon: 0318 - 521700	 HARDEMAN VEENENDAAL
Project: Nieuwbouw bedrijfshal	Schacht: 1:100	Fax: 0318 - 540601	Internet: www.harde-man.nl
TN Plastics - Ter Aar	Datum: 13.06.2025	Email: tekenkamer@harde-man.nl	Postbus 376 3900 AJ VEENENDAAL

Orderwerp:	Werknummer:	Bladnummer:
STAAL AANZICHTEN fase-B	44449	A11