




AANZICHT as-F

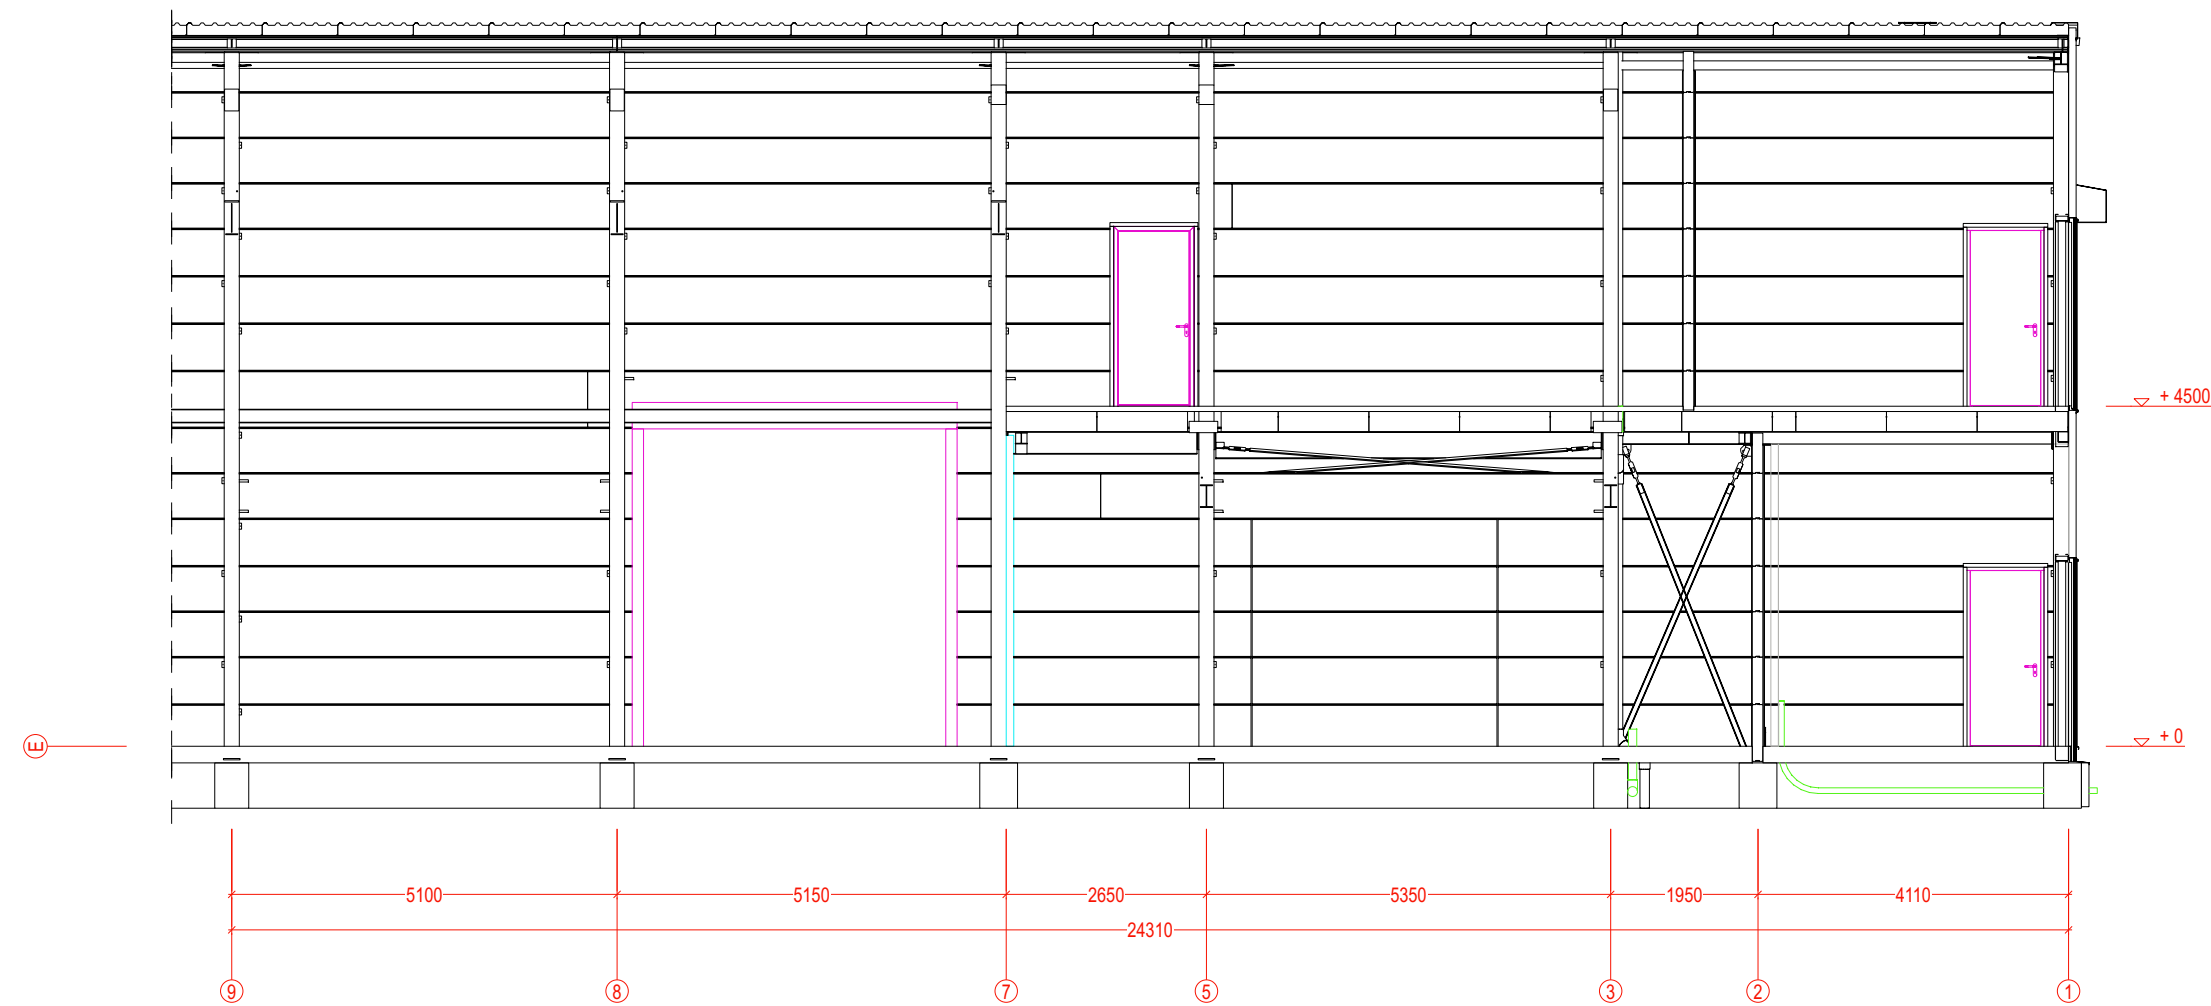


AANZICHT as-E

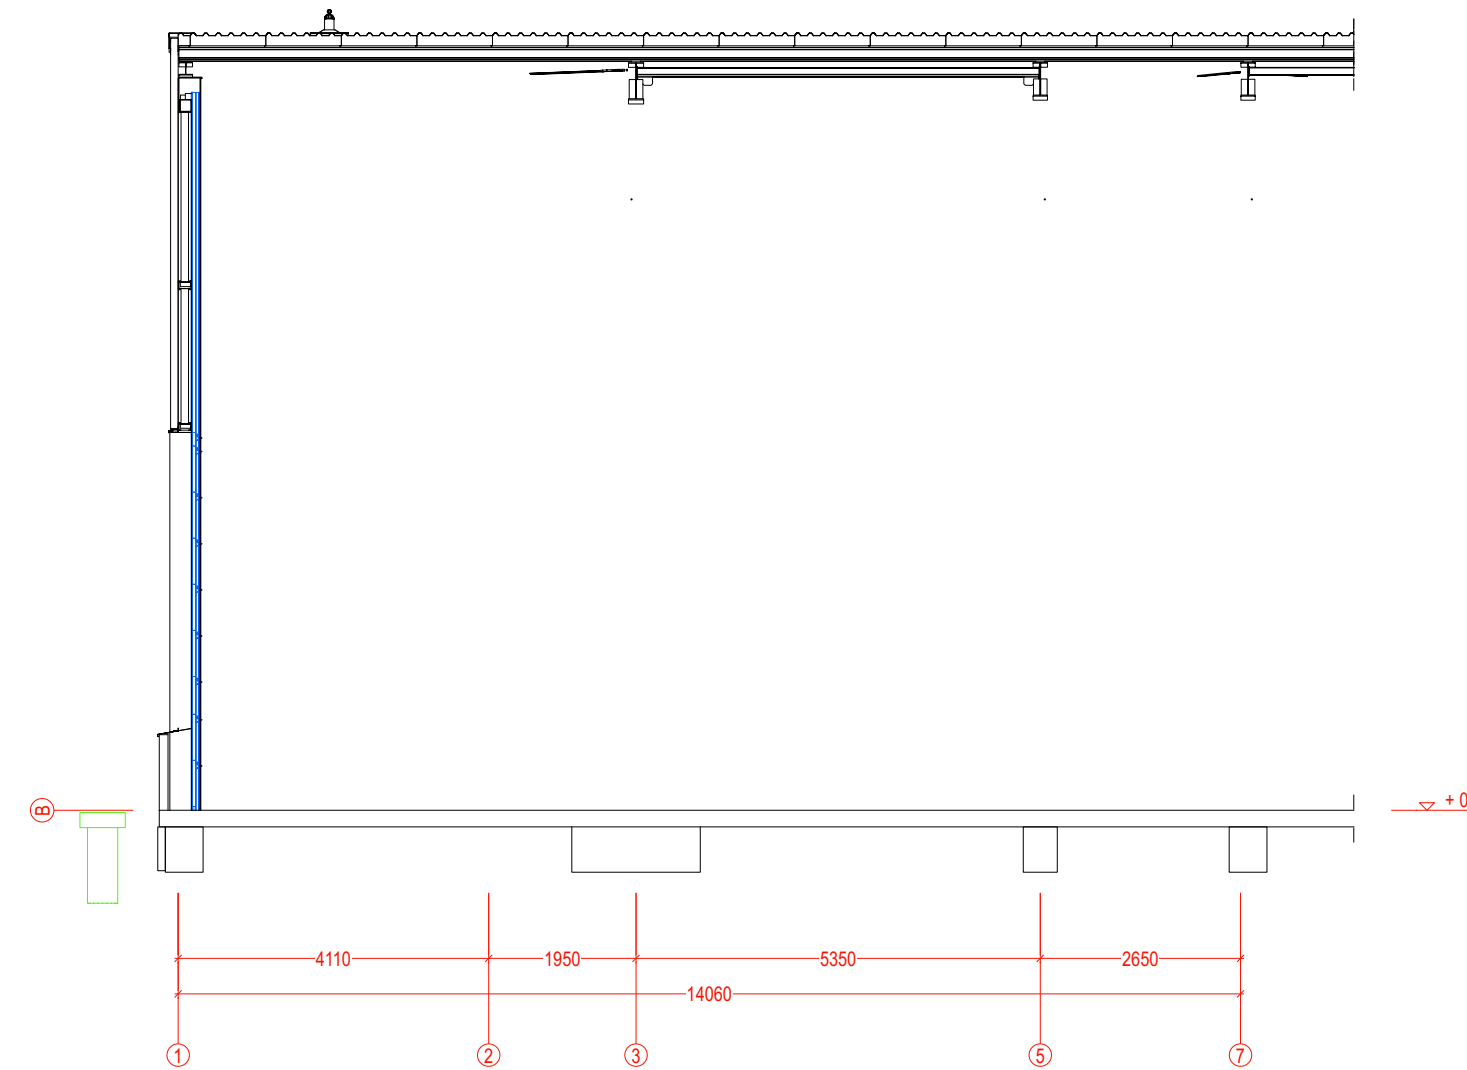


AANZICHT as-B

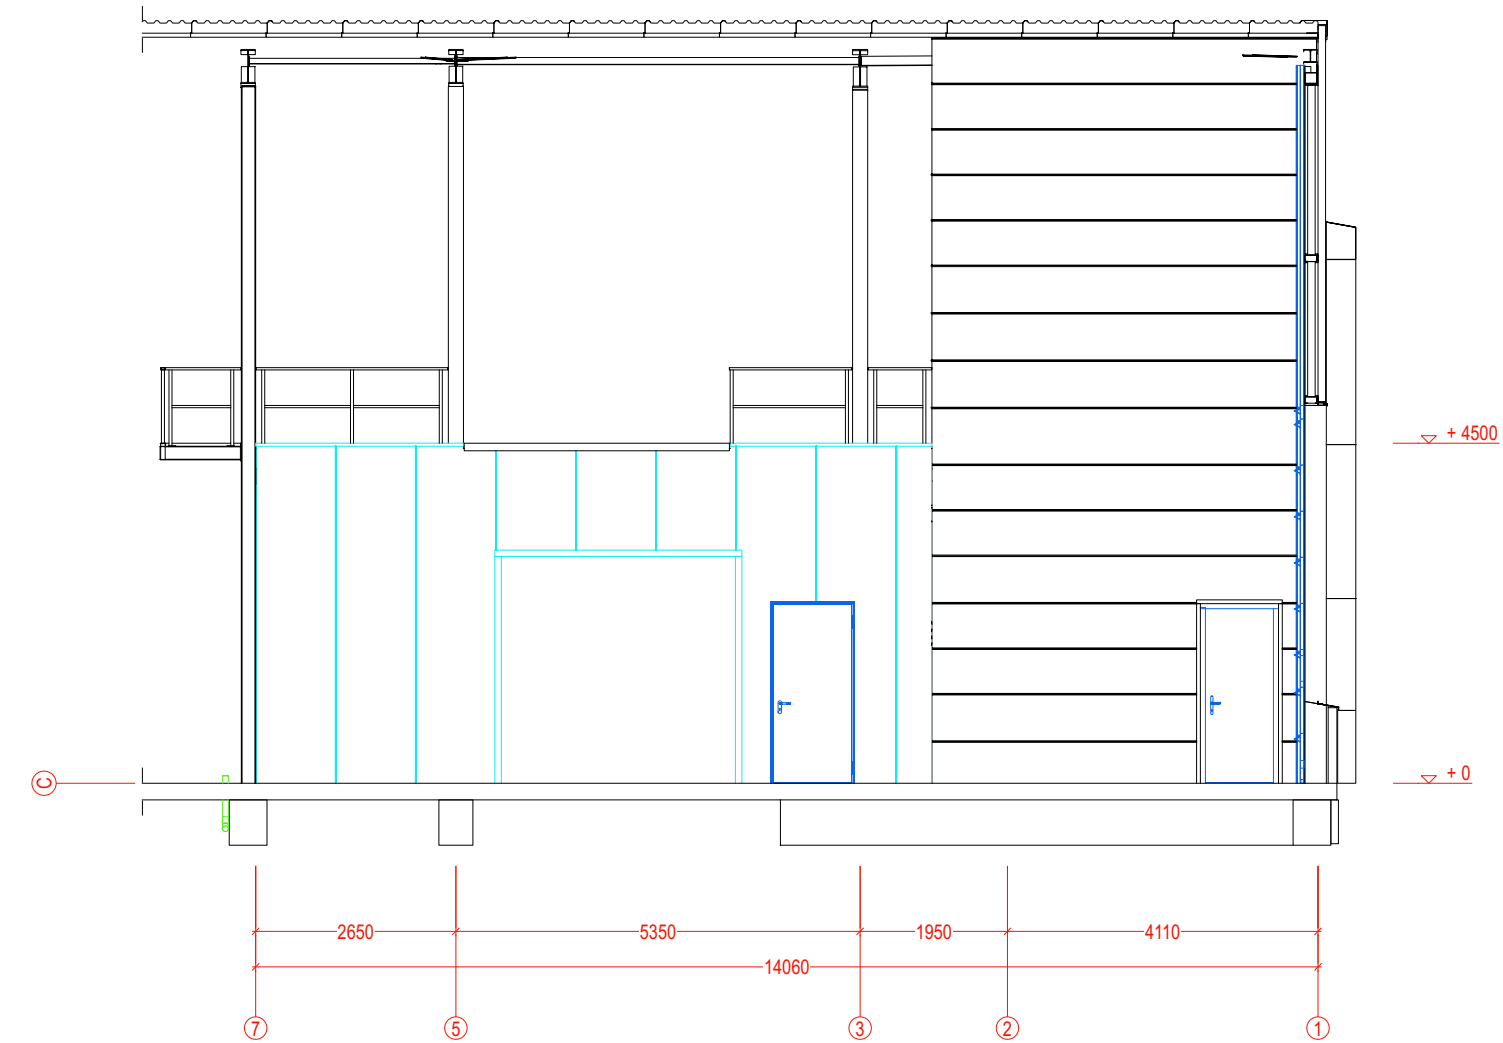


AANZICHT as-C

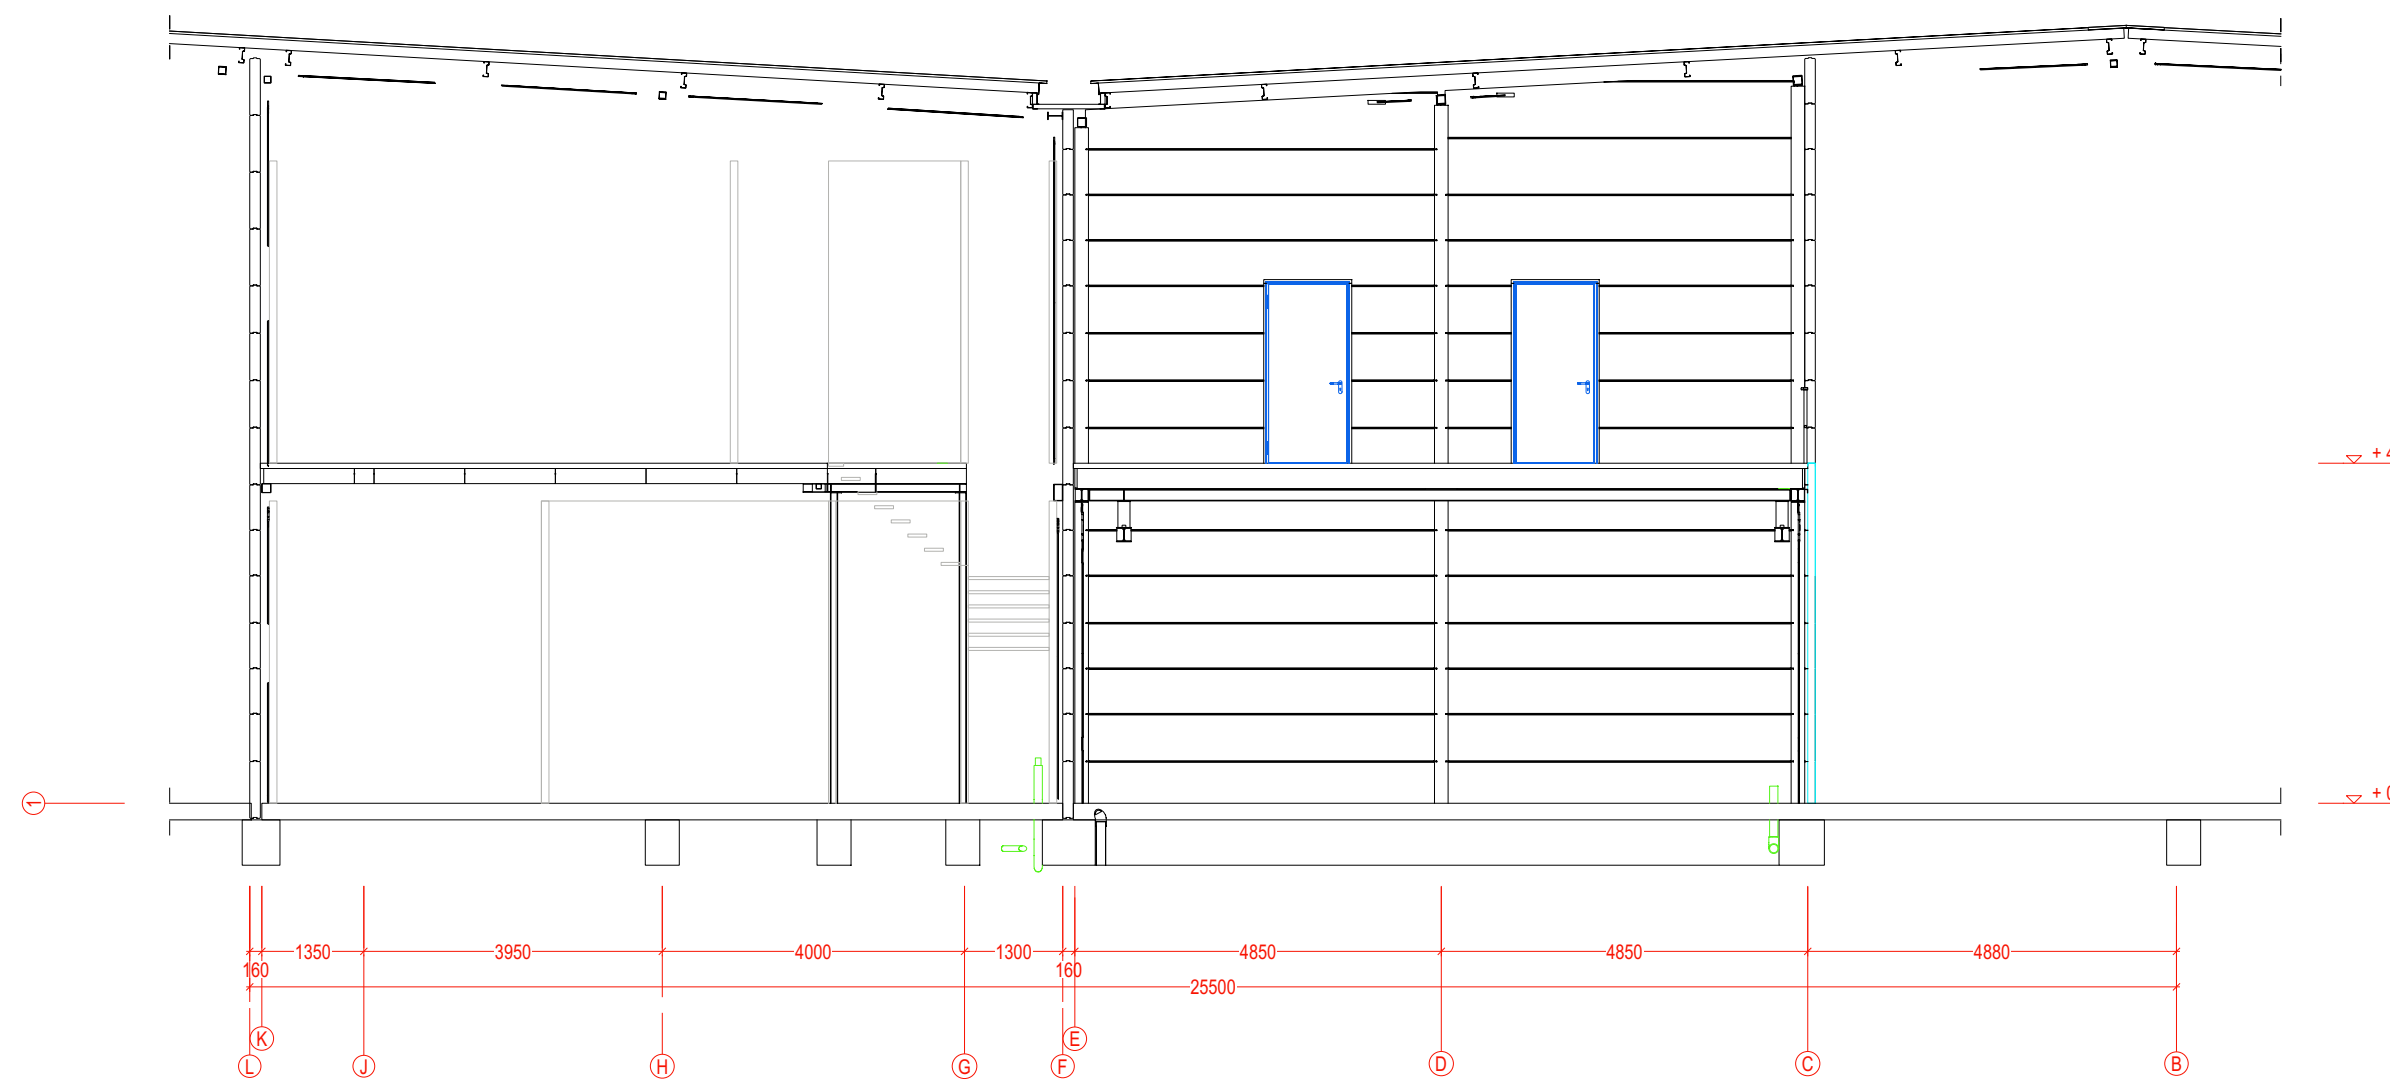

AANZICHT as-2/2'

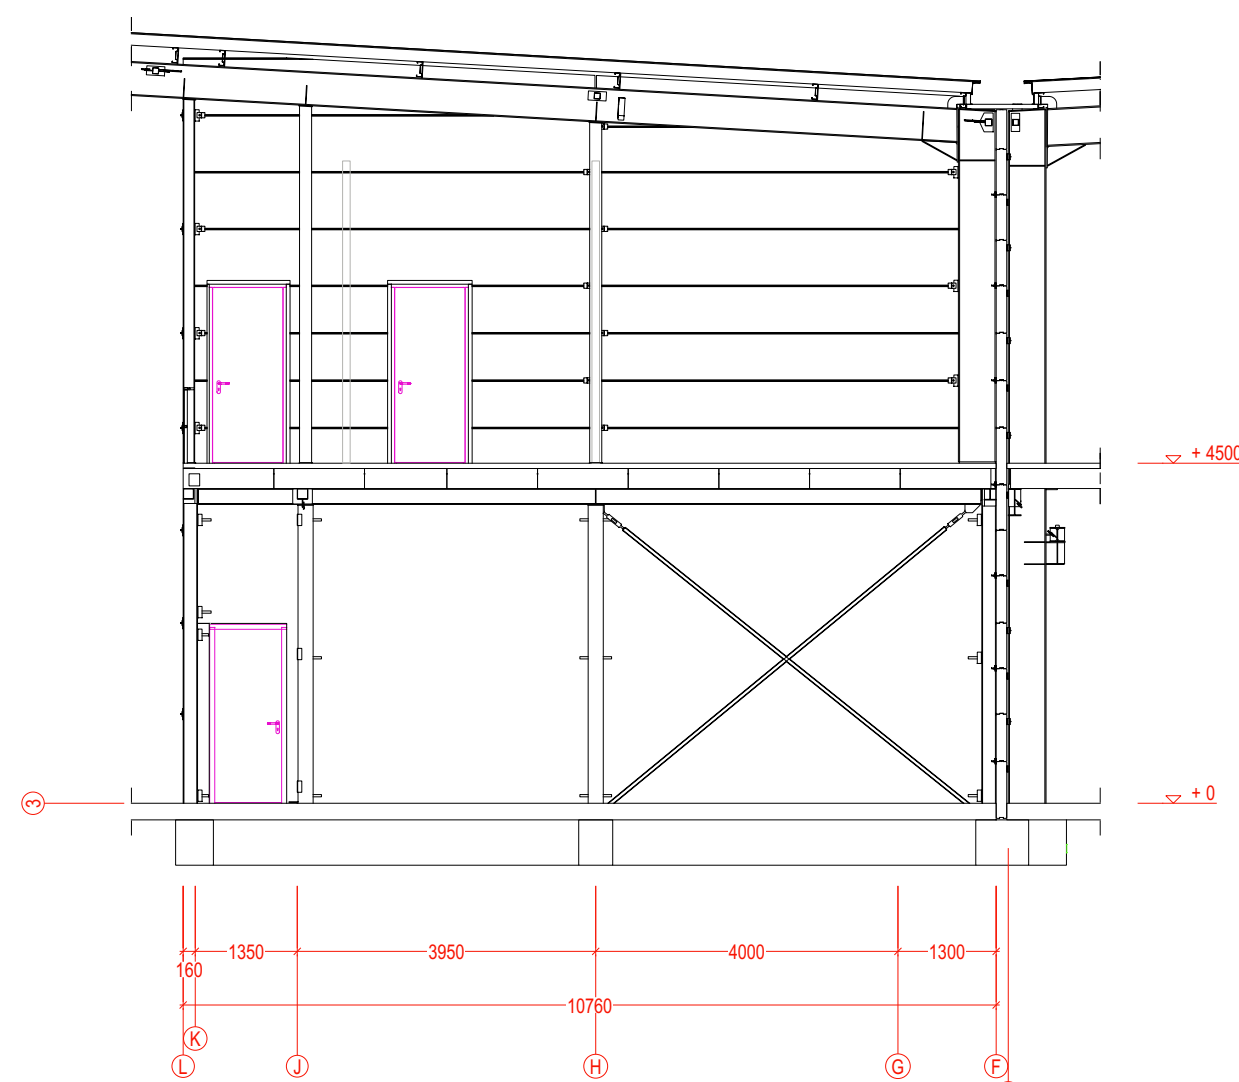

AANZICHT as-3

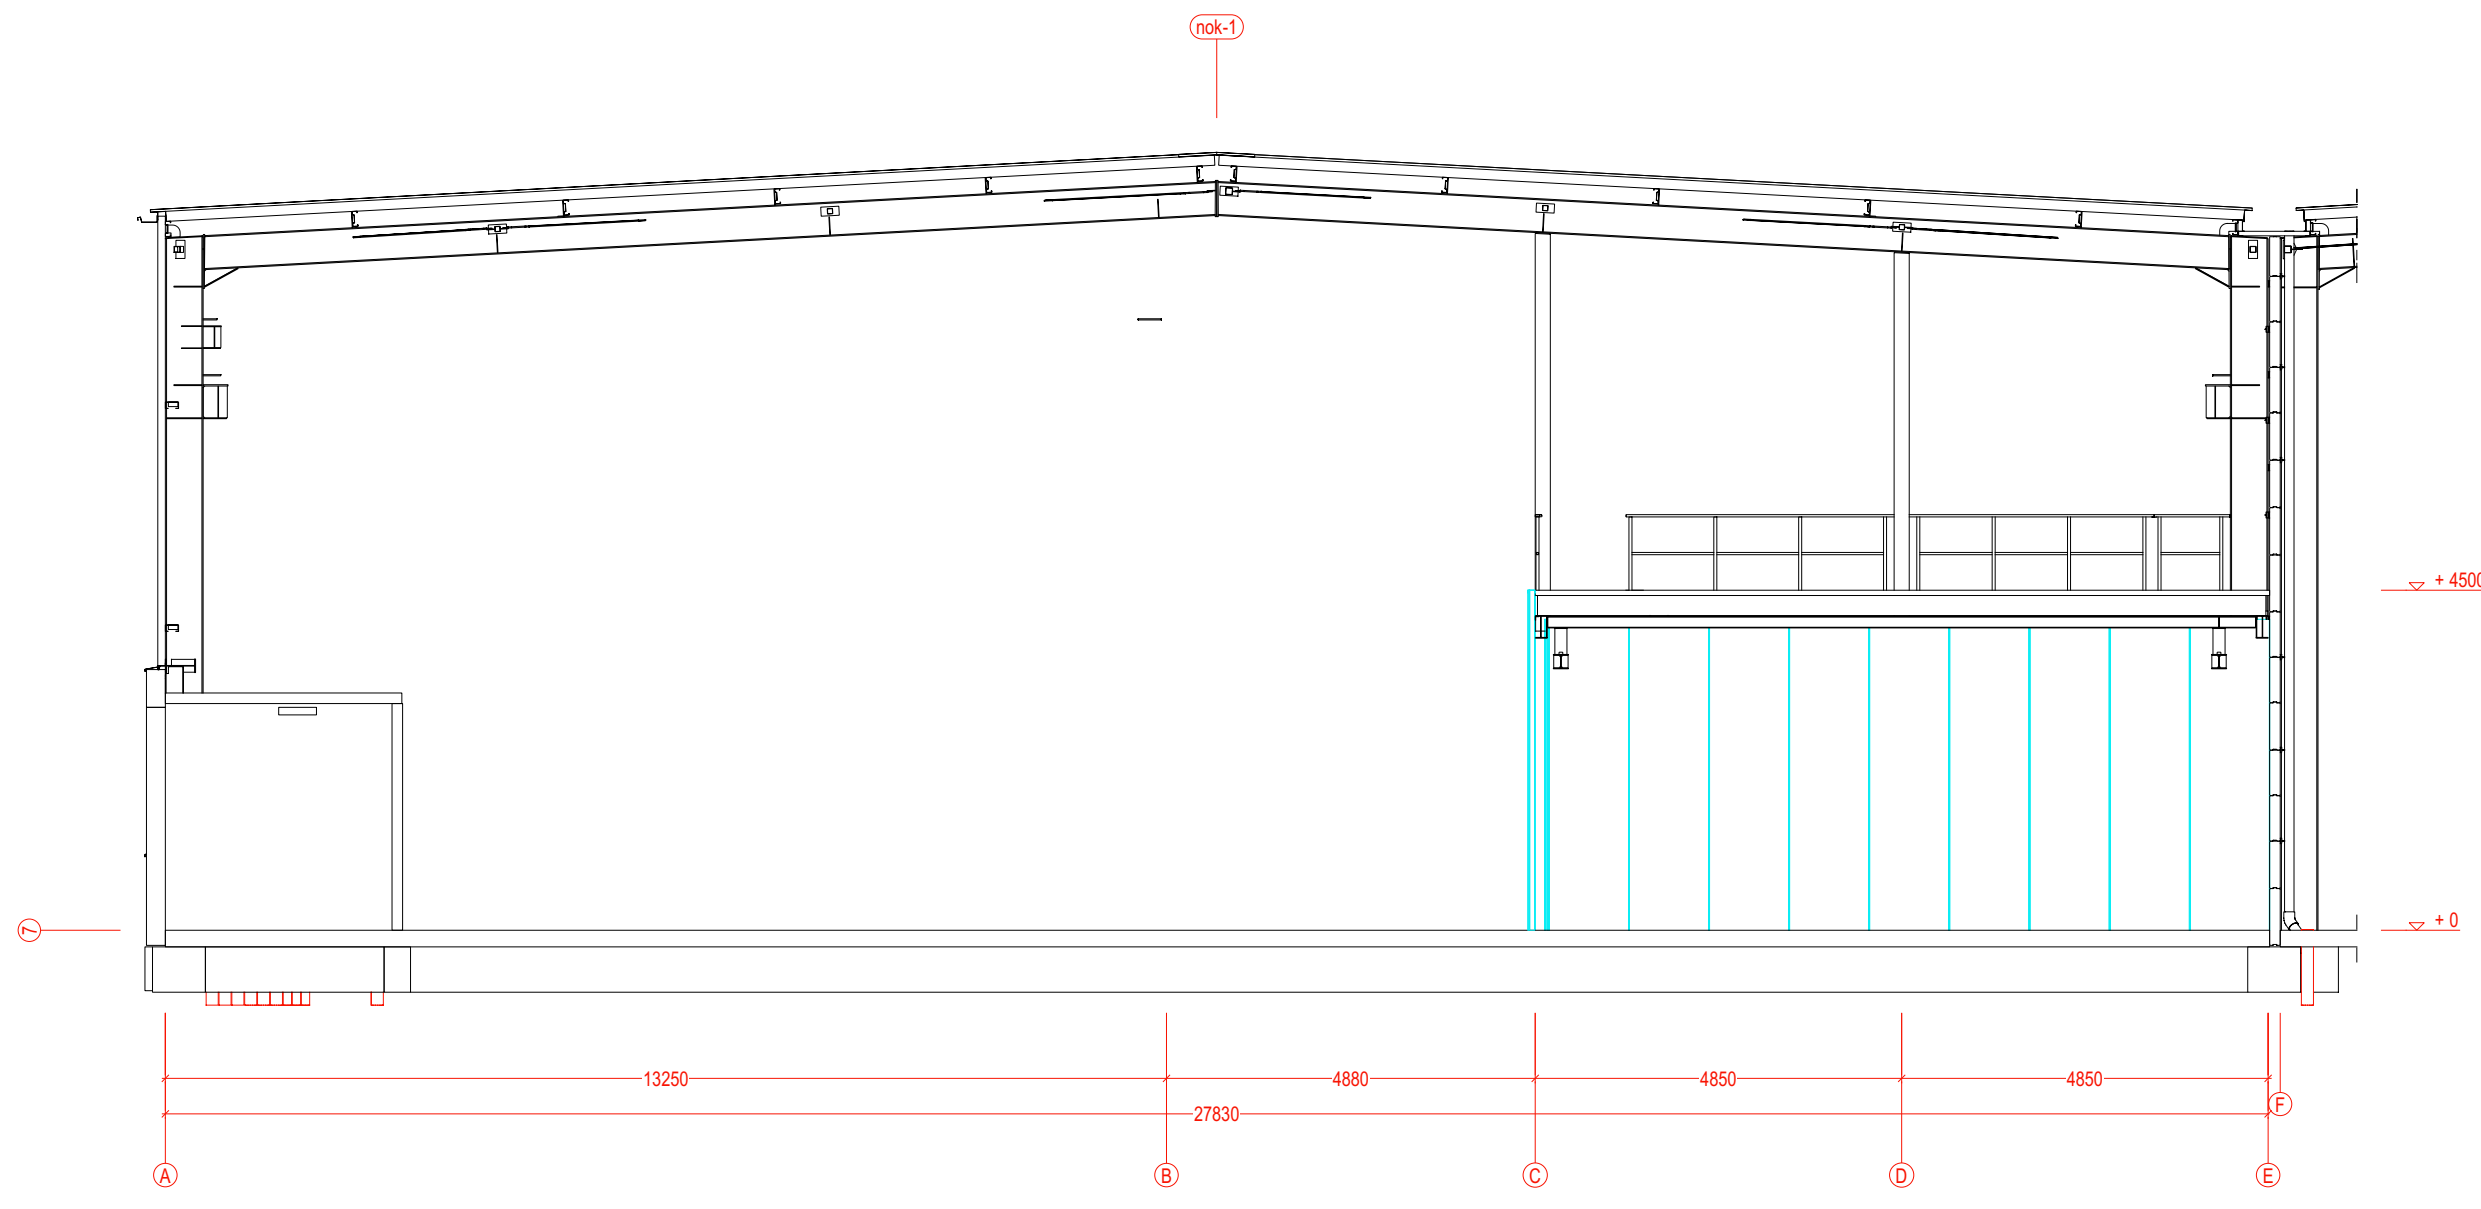

AANZICHT as-7

Opdrachtgever: Logvast Beheer BV Project: Nieuwbouw bedrijfsthal TN Plastics - Ter Aar		VOORLOPIG Ornaal: 1:100 Verenat: JPL Dat: 08.05.2025	HARDEMAN TECHNISCH Telofon: 0218 - 521700 Fax: 0218 - 640651 Email: www.hardeman.nl telefoon@hardeman.nl Postbus 376 3900 AJ VEENENDAAL
Ordercode: BINNENWANDEN		Index 44449 C5a	Datum: 24.07.2025